


Cozinha: o que cabe na linha e o que bloqueia a entrada

Planta em escala 1:20 | Atualiza a base A04.4 existente; preserva a sequencia escolhida

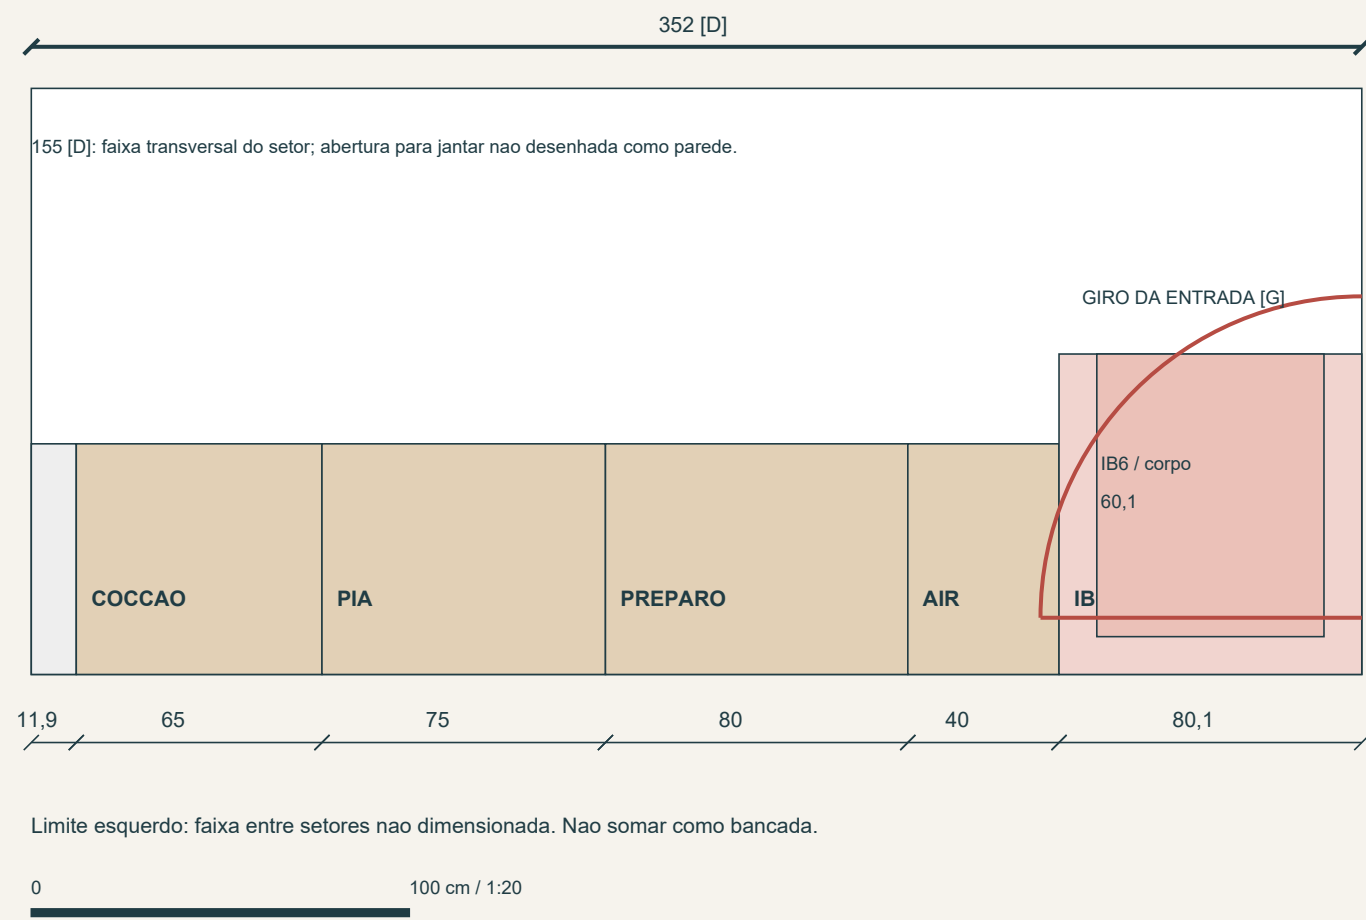

Base aproveitada

A01.2: cotas e leitura da planta oficial. A04.4 R00: reservas de aparelhos e desenhos sem escala. Distribuicao R01: metas de modulos e ordem definida. Esta revisao transforma a linha em teste cotado; nao duplica a concepcao.


Soma corrigida

65 + 75 + 80 + 40 + 80,1 = 340,1 cm. Restam 11,9 nos 352 documentais. Essa margem ainda precisa absorver paineis, ajustes e acabamentos; nao e espaco livre garantido.

Conflito identificado

A IB6 na extremidade cruza o giro grafico da porta, mesmo com sua largura corrigida. A reserva inclui 10 cm de cada lado. Desenho usa corpo e reserva separadamente; nenhuma inversao de porta foi aprovada.


Lavanderia: continuidade preservada, dimensionamento separado

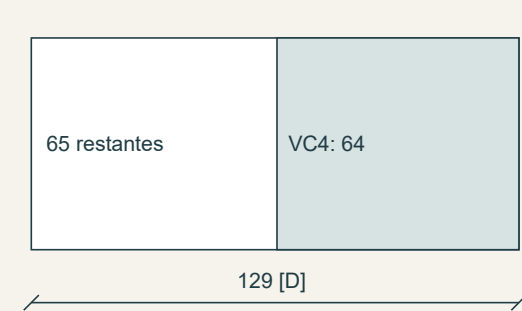

129 - 64 = 65 cm antes de tanque, shaft, paineis e tubulacoes. O desenho nao atribui os 65 integralmente ao tanque. Profundidade fechada da VC4 com reserva traseira: 72 cm; com porta a 90 graus: 120 cm. Na faixa de 154 cm restam 82 / 34 cm, sem incluir a pessoa. A faixa desconhecida entre setores impede tratar 129 + 352 como comprimento final da pedra.

Altura de 92 cm: conferir o conjunto, nao so a maquina

Elevacao em escala 1:20 | Alturas de aereos, pedra, forro e ferragens continuam pendentes

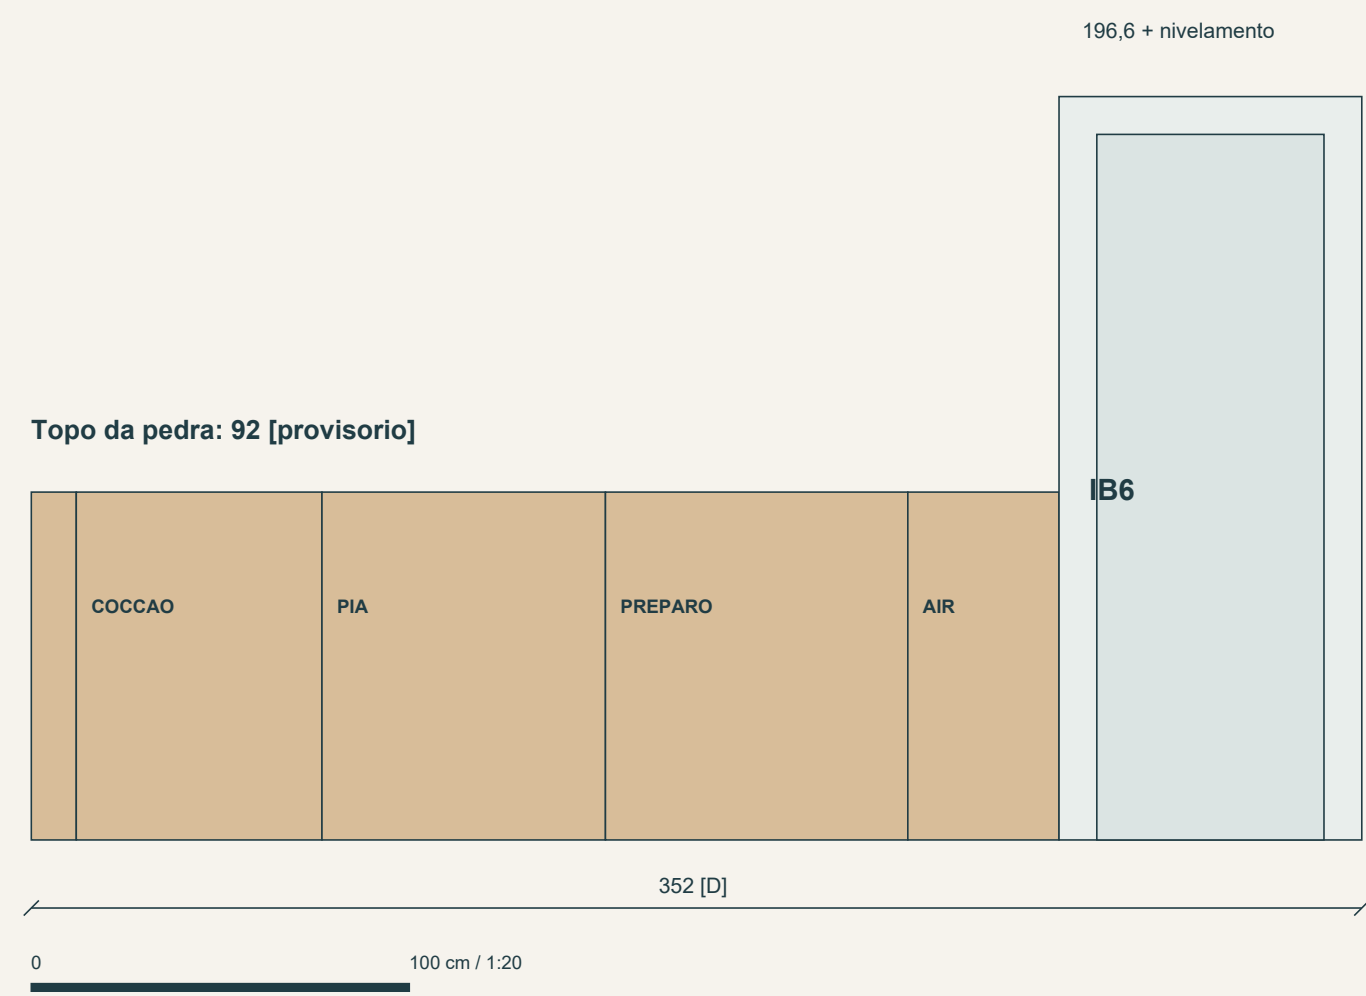

A elevacao mostra zonas; nao desenha nichos de forno ou aereos como aprovados.

Gaveta horizontal de limpeza

Continua como pedido funcional. Testar sob zonas secas, com recuo para os pes, sem ocupar ventilacao ou suporte do forno. Nao aumentar a bancada de 92 cm apenas para encaixar essa gaveta.

Lava e seca sob a pedra

Vao livre minimo registrado: 85,5 cm + nivelamento. Com topo a 92 cm, restam 6,5 cm para espessura da pedra, apoios que invadam o vao e ajuste de nivelamento. Exemplo apenas: pedra de 2 cm deixaria 4,5 cm para os demais descontos. Pedra de 2 cm nao foi escolhida.

Forno Venax sob o cooktop: altura critica

Corpo do forno GIII: 61 cm de altura. Manual Venax registrado exige 20 cm entre seu topo e o fundo do cooktop. Logo, $92 - 61 - 20 = 11$ cm para a elevacao da base do forno mais a distancia do topo da pedra ate o fundo do cooktop. Esse saldo ainda nao valida estrutura, ventilacao ou rodape.

Profundidade e abertura

Profundidade de 61 cm da bancada e hipotese de planta, nao dimensao final. Forno tem corpo com profundidade de 61,5 cm; verificar nicho, frente projetada, conexoes e ventilacao pelo manual. Nao forcar o equipamento no desenho. Porta do forno, gavetas e lixeira precisam de envelopes de abertura.

Aereos e eletrodomesticos de bancada

Micro-ondas ME23P permanece com divergencia de 10 cm desejados contra 30 cm superiores registrados no manual. Air fryer deve permanecer acessivel, mas seu modulo de 40 cm nao comprova afastamento termico junto da IB6. PE11X de 25 cm de largura precisa de lugar junto da pia, sem consumir silenciosamente os 80 cm de preparo.

Resultado e alternativas que merecem o proximo teste

Estudo de viabilidade dimensional | Nenhuma escolha fechada foi substituida

A / Manter todos os comprimentos propostos

Resultado: soma longitudinal de 340,1 cm cabe nos 352 cm apenas como soma. A porta impede aprovar a implantacao na extremidade. Portanto, a distribuicao anterior nao esta validada como cozinha utilizavel, apesar da margem de 11,9 cm.

B / Preservar aproximadamente 85 cm junto a entrada

Hipotese de reserva para a porta: $352 - 85 = 267$ cm na linha. Mantendo IB6 (80,1), cocção (65) e pia (75), sobram 46,9 cm para air fryer + preparo. Frente a meta conjunta de 120 cm, faltam 73,1 cm. Nao recomendo transformar esses 46,9 cm no preparo final: contraria sua prioridade de cozinhar bem.

C / Rever a posicao da IB6 na planta completa

E a frente de estudo mais promissora para preservar bancada, mas ainda nao ha posicao alternativa validada. Uma geladeira em frente ao jantar pode eliminar passagem; na lavanderia disputa espaco tecnico. A proxima comparacao deve redesenhar cozinha, entrada e jantar juntos, preservando a IB6 e explicitando qualquer alteracao de sequencia antes de fechar.

O que esta efetivamente pronto

Planta da sequencia atual em 1:20; elevacao de referencia em 1:20; correção da IB6; soma de modulos; orcamento de altura para maquina e forno; interface com lavanderia e lista de conflitos. Nao foram inventadas cotas de pontos, shaft ou aereos.

O que continua pendente

Implantacao que resolva a entrada; envelopes reais de portas e gavetas; nichos e afastamentos dos equipamentos; cuba/torneira; apoios da pedra; medidas acabadas e infraestrutura. A mesa arredondada e o jantar de seis lugares permanecem como requisitos.

Fontes locais e hierarquia

Planta baixa oficial.pdf; A01.2_Memorial_e_pendencias_R00.md; A04.4_Implantacao_preliminar_R00.pdf (historico); A04.4_Quadro_de_medidas_e_reservas_R00.md; A04.4_Conferencia_e_continuidade_R00.md; A04.4_Distribuicao_cozinha_proposta_R01.md; registro mestre v0.6 e A04.6 R01. [D] documental; [G] grafico aproximado; demais medidas de moveis sao propostas. Fontes de manuais e paginas detalhadas nesses documentos. Esta revisao corrige/atualiza R00, sem alterar os documentos oficiais.