


O giro do quarto disputa espaço com o guarda-roupa


Comparação em 1:25 | Duas portas externas iguais nos cenários; muda o fechamento do dormitório

A / Porta de abrir no novo batente

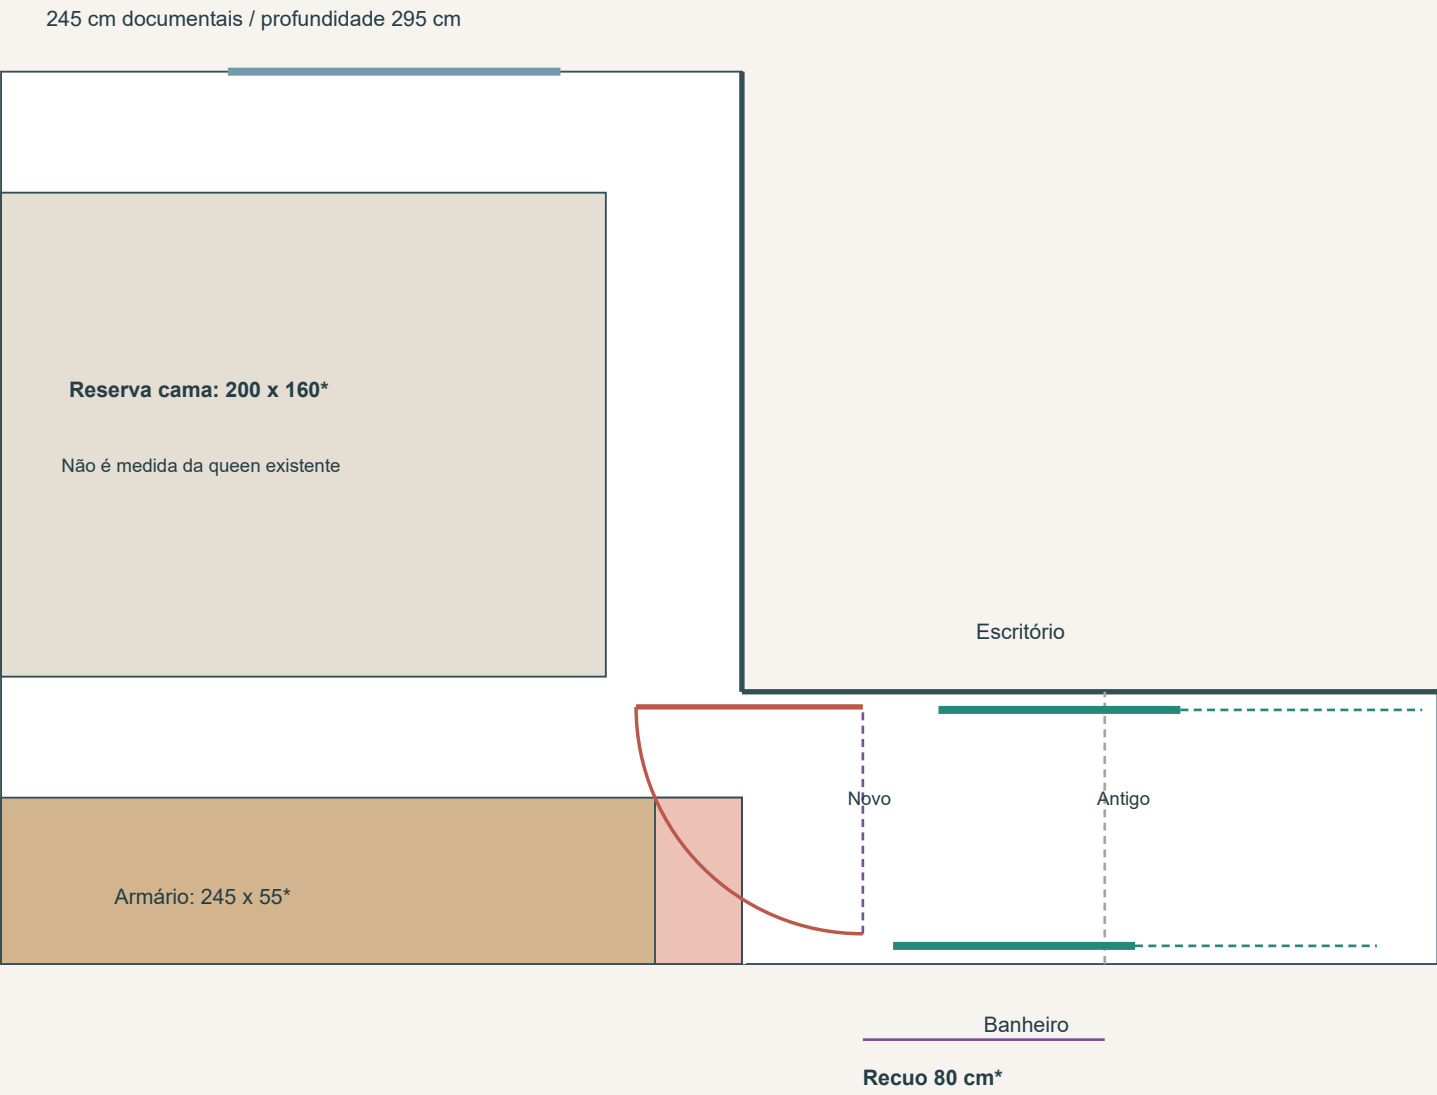

A: conflito com a ponta do armário
Com folha ideal de 75 cm, o guarda-roupa teria de terminar em aproximadamente 216 cm, antes de folgas reais. Perda de cerca de 29 cm em relação ao armário hipotético de 245 cm. Não aprovar corte de marcenaria por este desenho.

B / Articulada no novo batente

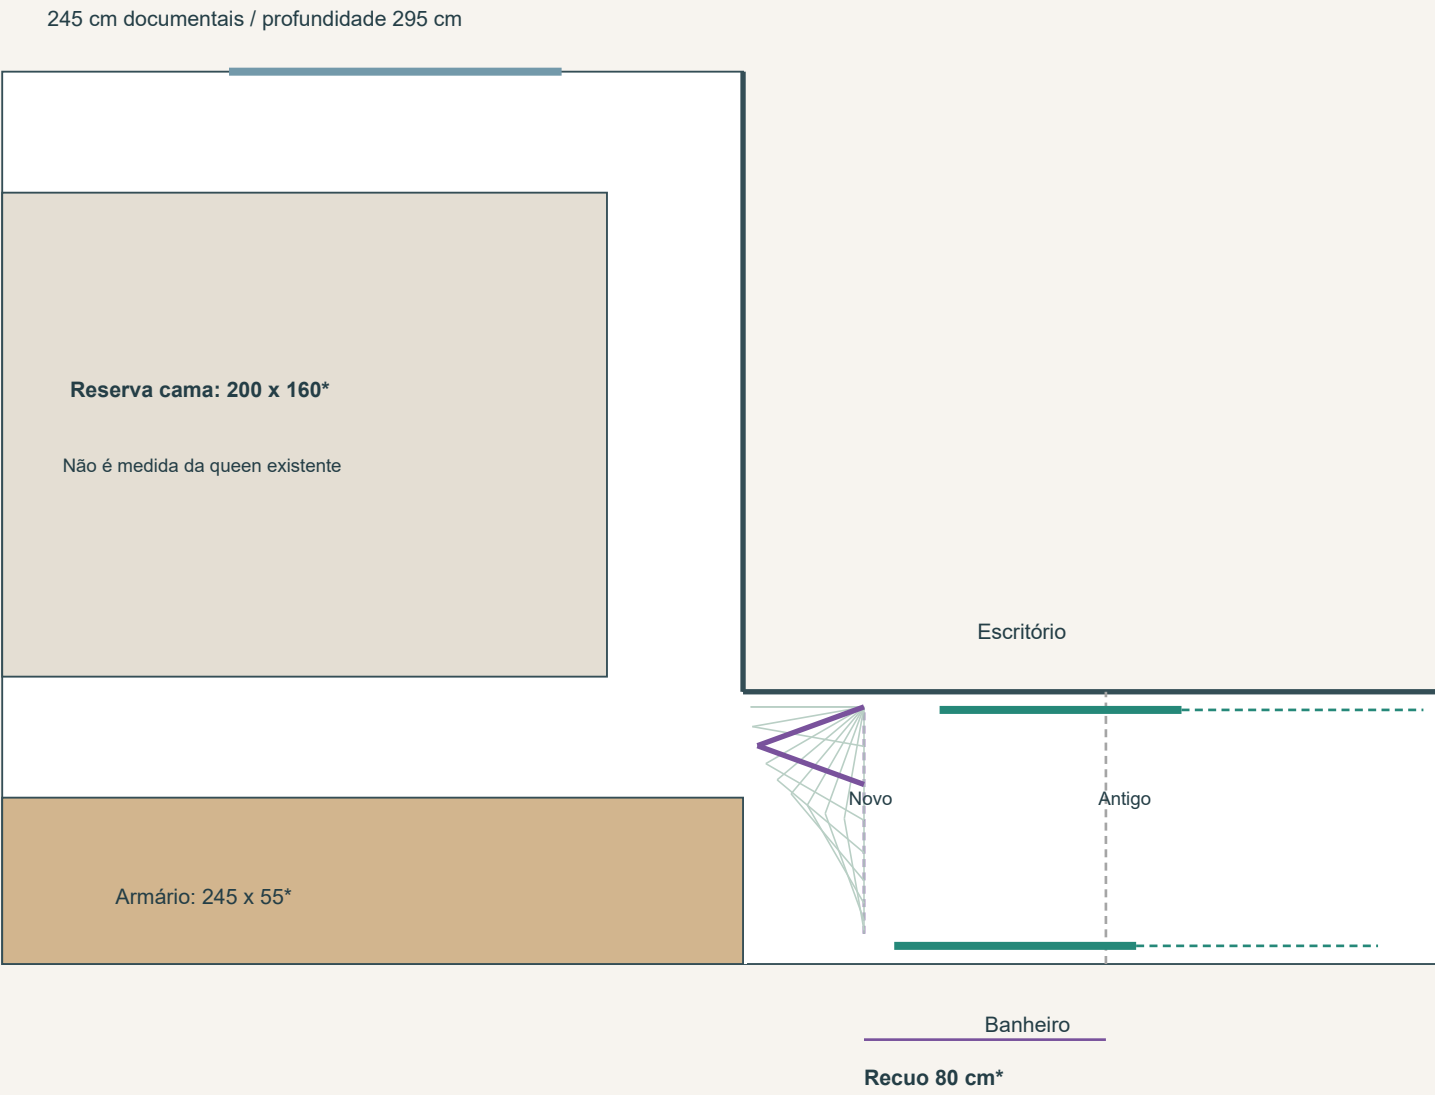

B: melhor hipótese para preservar armazenamento
Duas metades ideais de 37,5 cm não cruzam o armário neste ensaio. Ainda faltam pacote dobrado, puxadores, batente e largura útil. O modelo articulado não está escolhido.

O que esse teste comprova - e o que permanece aberto

Hipóteses explícitas evitam transformar um desenho que cabe em medida executiva

Base documental
Dormitório: 245 x 295 cm. Circulação: cota de 90 cm na planta. Estação do escritório continua de frente para a janela.

Hipóteses usadas
Acesso do quarto: comprimento aproximado de 120 cm por leitura gráfica. Recuo testado: 80 cm, não aprovado. Porta do quarto: 75 cm, eixo a 85 cm da parede inferior. Duas folhas externas de 80 cm, sem modelo. Móveis: armário 245 x 55 e cama 200 x 160 cm, apenas reservas de ensaio.

Por que testar 80 cm de recuo
Neste modelo, a folha externa mais próxima do quarto termina em x295; o novo fechamento está em x285. São 10 cm de reserva gráfica, antes da compatibilização de batente/puxador. Recuar só 60 cm deixaria o novo fechamento em x305, sobre o espaço da folha aberta. As posições reais dos vãos podem alterar esse resultado.

Preferência preliminar: duas portas externas + entrada recuada + articulada no dormitório é a combinação que melhor preserva o armário neste ensaio. Depende de levantamento, aprovação técnica, produto real e orçamento. A porta de abrir segue alternativa se o ganho justificar reduzir/redistribuir a marcenaria.

Impacto no dormitório
A cama não cruza as trajetórias desenhadas, mas suas medidas externas ainda não foram levantadas. No ensaio, sobram somente 40 cm entre cama e frente do armário e 45 cm aos pés: pontos estreitos que precisam de estudo próprio. Não é aprovação do layout do quarto.

O recuo transforma aproximadamente 0,72 m² (80 x 90 cm) da entrada privativa em circulação, sem criar área nova. As folhas usam as laterais desse trecho.

As duas portas externas
Trilhos independentes e folhas em faces opostas. Exemplo com projeção total de 6 cm de cada sistema sobre o corredor de 90 cm: restam 78 cm. Se precisarem de 10 cm por lado para vencer ressaltos, restam 70 cm. Nenhum desses valores está aprovado. Medir o conjunto completo e não apenas a espessura da folha.

Teto total: R\$ 10.000, incluindo o novo fechamento

Distribuição de verba proposta | Não é cotação nem confirmação de execução pela Cury

Duas portas de correr novas, ferragens e instalação	R\$ 4.000
Porta articulada do quarto, batente e instalação	R\$ 1.800
Recuo / novo fechamento e adequações locais	R\$ 1.200
Acabamentos, retirada, descarte e transporte	R\$ 800
Levantamento e avaliação técnica / documentação	R\$ 700
Subtotal a buscar nas cotações	R\$ 8.500
Reserva para imprevistos	R\$ 1.500
Teto autorizado por Elias	R\$ 10.000

Condição financeira
Buscar propostas completas até R\$ 8.500 para manter R\$ 1.500 de reserva. As parcelas são metas de negociação, não preços pesquisados de serviços específicos. Se o total ultrapassar R\$ 10 mil, revisar o escopo antes de contratar. Sem descontar reaproveitamento ou eventual crédito da construtora.

- O que perguntar à Cury
1. Pode entregar a entrada do dormitório recuada, conforme estudo?
 2. Os encontros do batente antigo são removíveis sem alterar alvenaria estrutural?
 3. Pode fornecer cotas acabadas e detalhes de reforço/fixação e pontos elétricos afetados?
 4. Qual o prazo, valor total, escopo, garantia e documentação para executar ou autorizar?

Fontes: planta oficial P01; referência quarto1.png; F47-F51. Fonte do princípio articulado: Pormade, porta camarão (07/02/2024). Dimensões e cálculo de giro são hipóteses próprias; não especificação do fabricante.

Não foi localizada confirmação de que a Cury ofereça esta personalização no Guedala Park III. Consulta preparada, não enviada. Se houver intervenção estrutural, este estudo e esta verba deixam de bastar.

Estudo preliminar de 11/09/2026. Compatibilização de circulação, privacidade, umidade do banheiro, ferragens e manutenção pendente.