


Seis lugares: encaixe possível, ainda condicionado

Base oficial + hipóteses explícitas | Escopo: jantar, interface com sala, cozinha e entrada

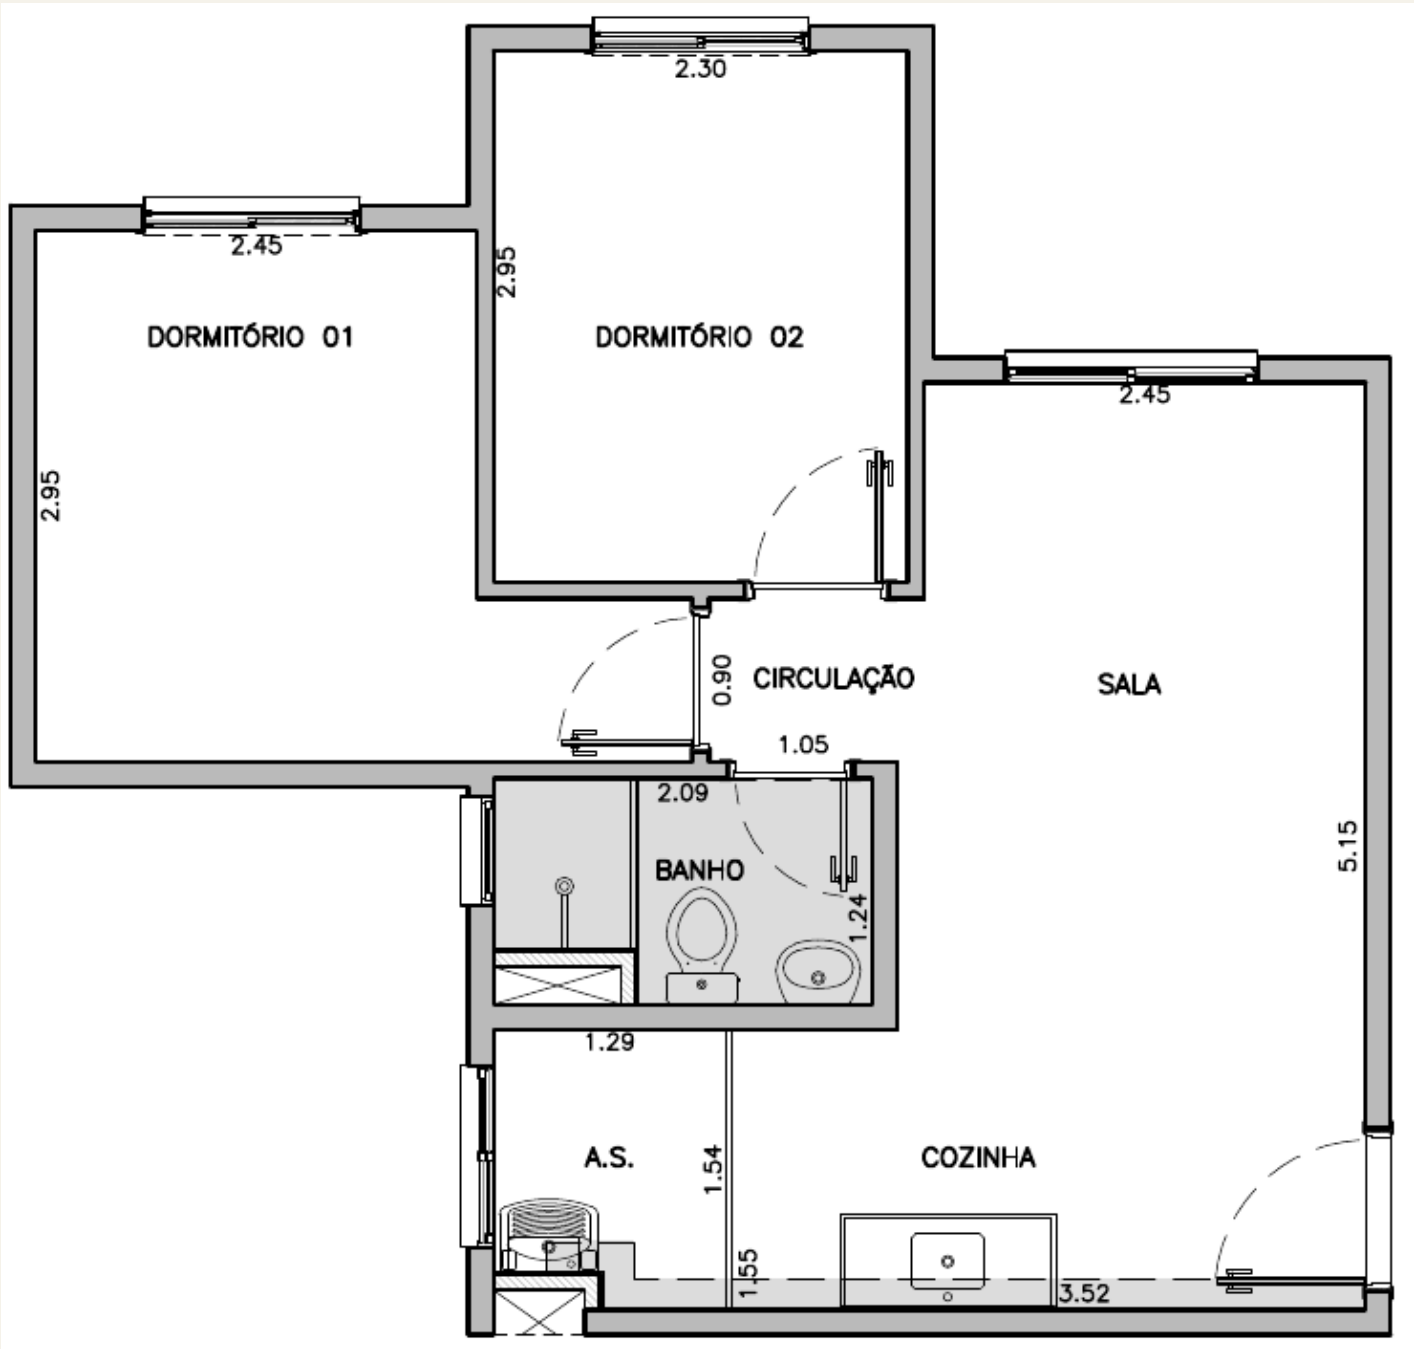

Recorte da planta oficial, apenas para leitura: sem escala de impressao nesta pagina.

O que foi conferido

A cota 245 corresponde a largura superior da sala. A cota 515 vai da parede da janela ate a parede da cozinha: nao e comprimento exclusivo de sala e jantar. A propria planta admite variacoes pelos acabamentos.

Resultado principal

Mesa fixa proposta de 180 x 75, banco reto de 180 x 55 e tres cadeiras sem bracos. O conjunto cabe geometricamente na faixa conservadora de 245, mas deixa apenas 65 atras das cadeiras no cenario sentado adotado. Nao equivale a conforto validado para duas horas.

Restricao encontrada



A reserva da geladeira no extremo junto a entrada se sobrepoe ao giro grafico da porta neste teste. A interface cozinha/entrada precisa ser resolvida antes de aprovar o layout completo. Nenhum equipamento ou ponto foi alterado.

Como ler as medidas

[D] cota documental. [P] proposta de movel ou envelope de uso. [G] estimativa grafica. [C] calculo condicionado as hipoteses. As pranchas 2, 4 e 5 possuem escalas fisicas declaradas; imprimir A3 a 100%, sem ajustar.

Uso diario e seis pessoas sentadas

Plantas esquematicas em escala 1:25 no A3 a 100% | Todas as dimensoes de moveis sao propostas

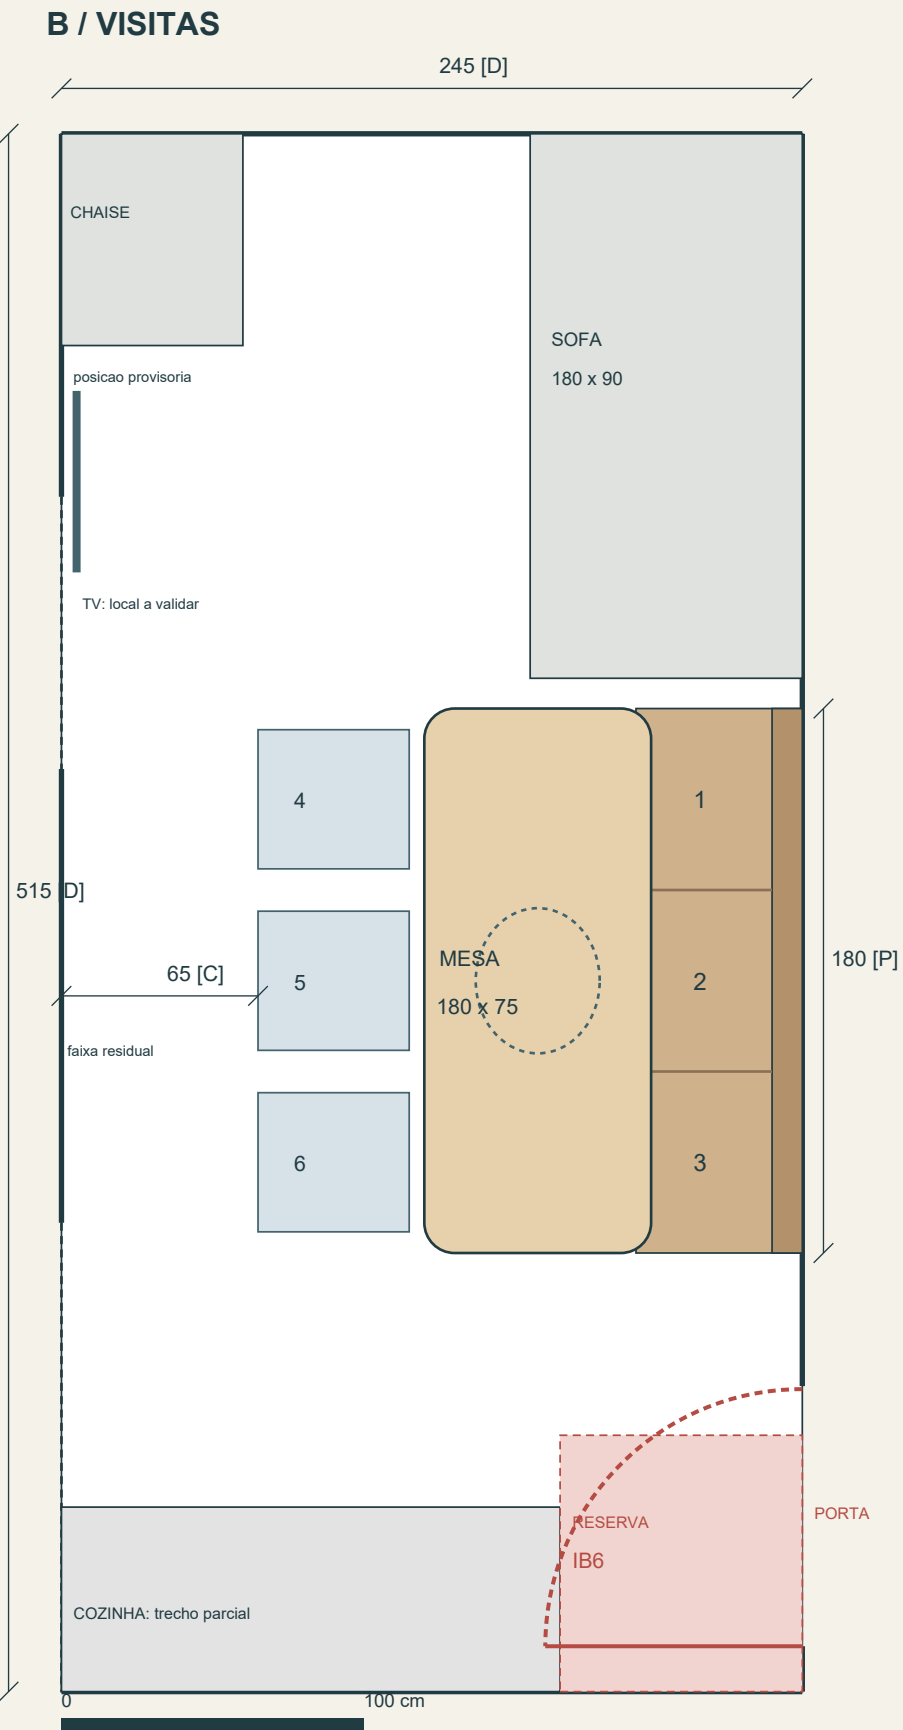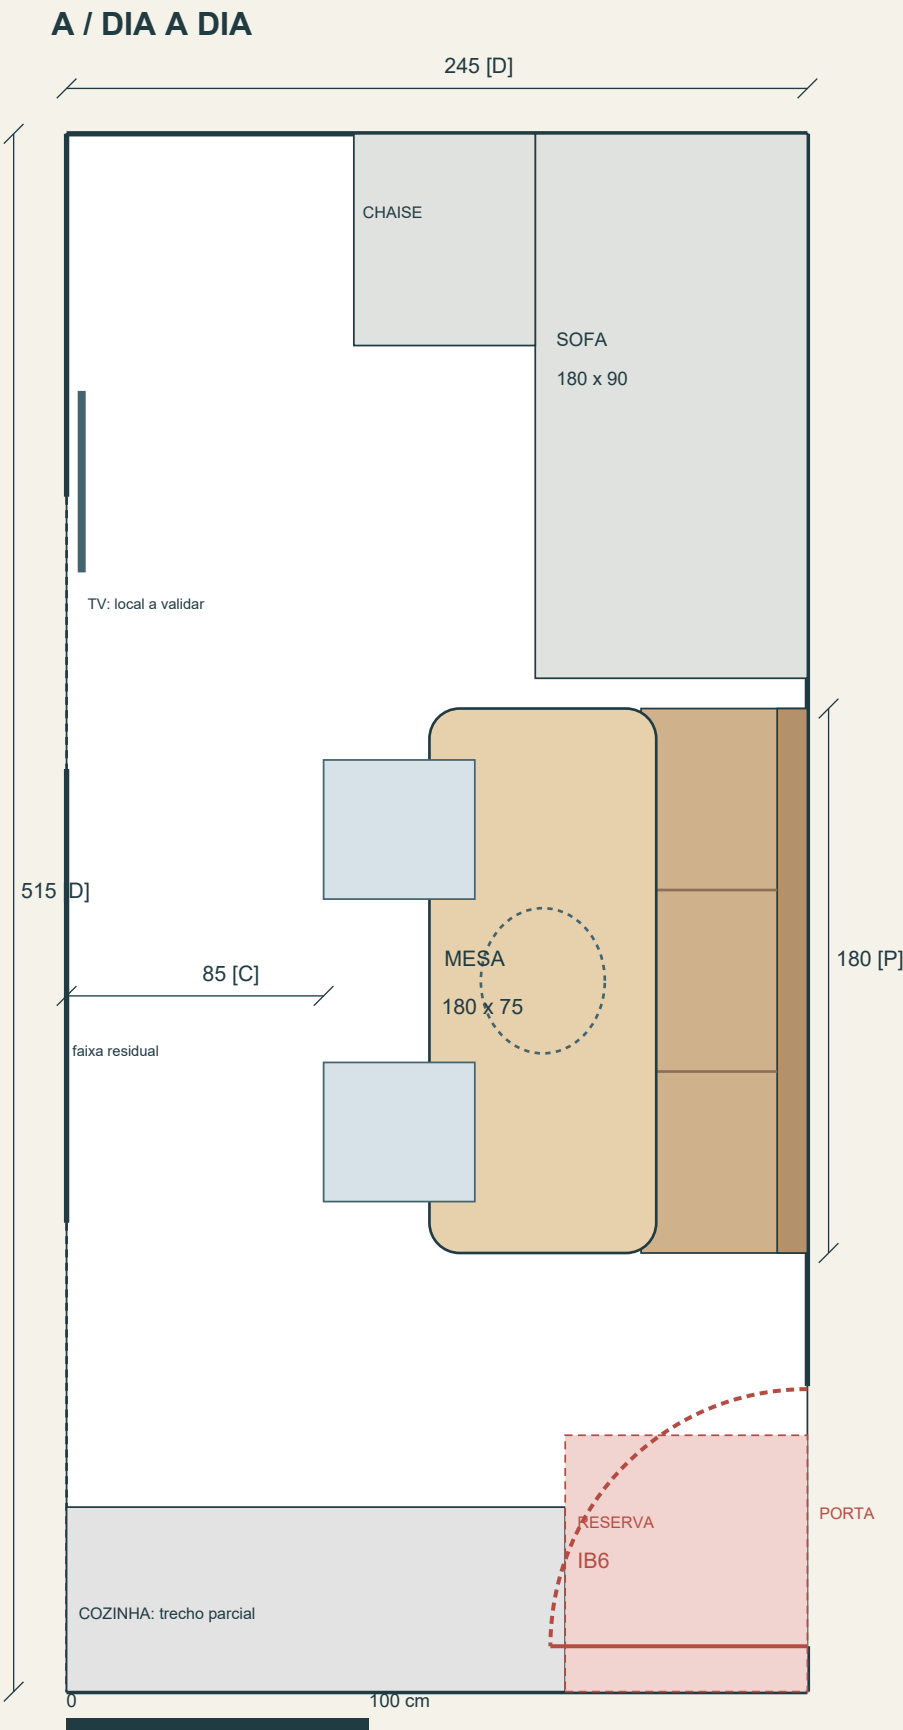

85 cm no modo recolhido

245 - 50 (parede a borda) - 75 (tampo) - 35 (cadeira recolhida) = 85. Nao representa duas pessoas sentadas. Ao usar uma cadeira, aplicar o envelope ocupado.

65 cm no modo ocupado

Com 55 da borda da mesa ate as costas da pessoa/cadeira: 245 - 50 - 75 - 55 = 65. Passagem apertada; nao e rota acessivel nem aprovacao normativa.

Tres pessoas no banco

180 / 3 = 60 de frente nominal por pessoa. Banco com 55 totais, sendo 10 reservados ao encosto e 45 ao assento. Estofamento, altura e cantos podem reduzir o uso real.

Acesso pelo lado da cozinha

Banco vai de y=190 a y=370. Reserva IB6 inicia em y=430,25: intervalo de 60,25. Essa aproximacao depende da posicao final da geladeira; o conflito na entrada impede valida-la.

Sala e terceira cadeira

Sofa 180 x 90 e chaise 60 x 70 sao envelopes de teste. A chaise deslocada fica provisoriamente junto a janela. Terceira cadeira fora deste recorte no cotidiano: ambiente ainda nao definido. TV nao tem destino aprovado.

Medidas propostas e limites de conforto

Comparacao numerica | Mesma parede a borda de 50 cm e envelope ocupado de 55 cm

Comparacao das mesas fixas

Tampo [P]	Frente/pessoa [C]	Faixa residual [C]	Leitura
160 x 75	53,3 cm	65 cm	Mais curta; pior para 3 alinhados.
180 x 70	60 cm	70 cm	Ganha 5 cm; tampo mais estreito.
180 x 75	60 cm	65 cm	Melhor equilibrio inicial; condicionado.
180 x 80	60 cm	60 cm	Mais apoio, pior passagem.
190 x 75	63,3 cm	65 cm	Consome mais 10 cm longitudinais.

Sensibilidade: o corpo e a cadeira mudam o resultado

Com tampo de 75, um envelope ocupado de 50 / 55 / 60 cm deixa respectivamente 70 / 65 / 60 cm. Se a largura real for 240, com envelope de 55, a faixa cai para 60 cm. Se banco e borda precisarem avançar mais 5 cm, perde-se mais 5 cm. Nao contar o recuo grafico do banheiro como folga garantida.

Movimentar a mesa tem um custo

Afastar a mesa 15 cm da parede para facilitar entrada no banco reduz a faixa ocupada de 65 para 50 cm. Com uma cadeira recuada mais 25 cm para levantar, sobram 40 cm no mesmo alinhamento. Portanto, entrada/saida e passagem nao podem ser consideradas simultaneamente confortaveis. Reposicionar com lugares desocupados e recolher depois.


Critérios usados, sem transformar recomendacao em norma

Adotados 60 cm de frente por pessoa e envelopes de cadeiras explicitamente propostos. A referencia comercial Room & Board recomenda 18-24 polegadas por lugar (aprox. 46-61 cm) e 36 polegadas de folga ao redor da mesa (aprox. 91 cm); sao orientacoes de mobiliario, nao normas brasileiras. Neste arranjo, mesa ate limite oposto = 120 cm; descontar pessoa/cadeira e indispensavel para avaliar passagem real.

Fonte: roomandboard.com/design/inspiration/dining-kitchen/how-to-design-a-dining-room | consulta 11/09/2026

Entrada: interferencia que impede fechar o conjunto

Detalhe em escala 1:15 no A3 a 100% | Porta por leitura grafica; reserva IB6 transcrita do quadro A04.4

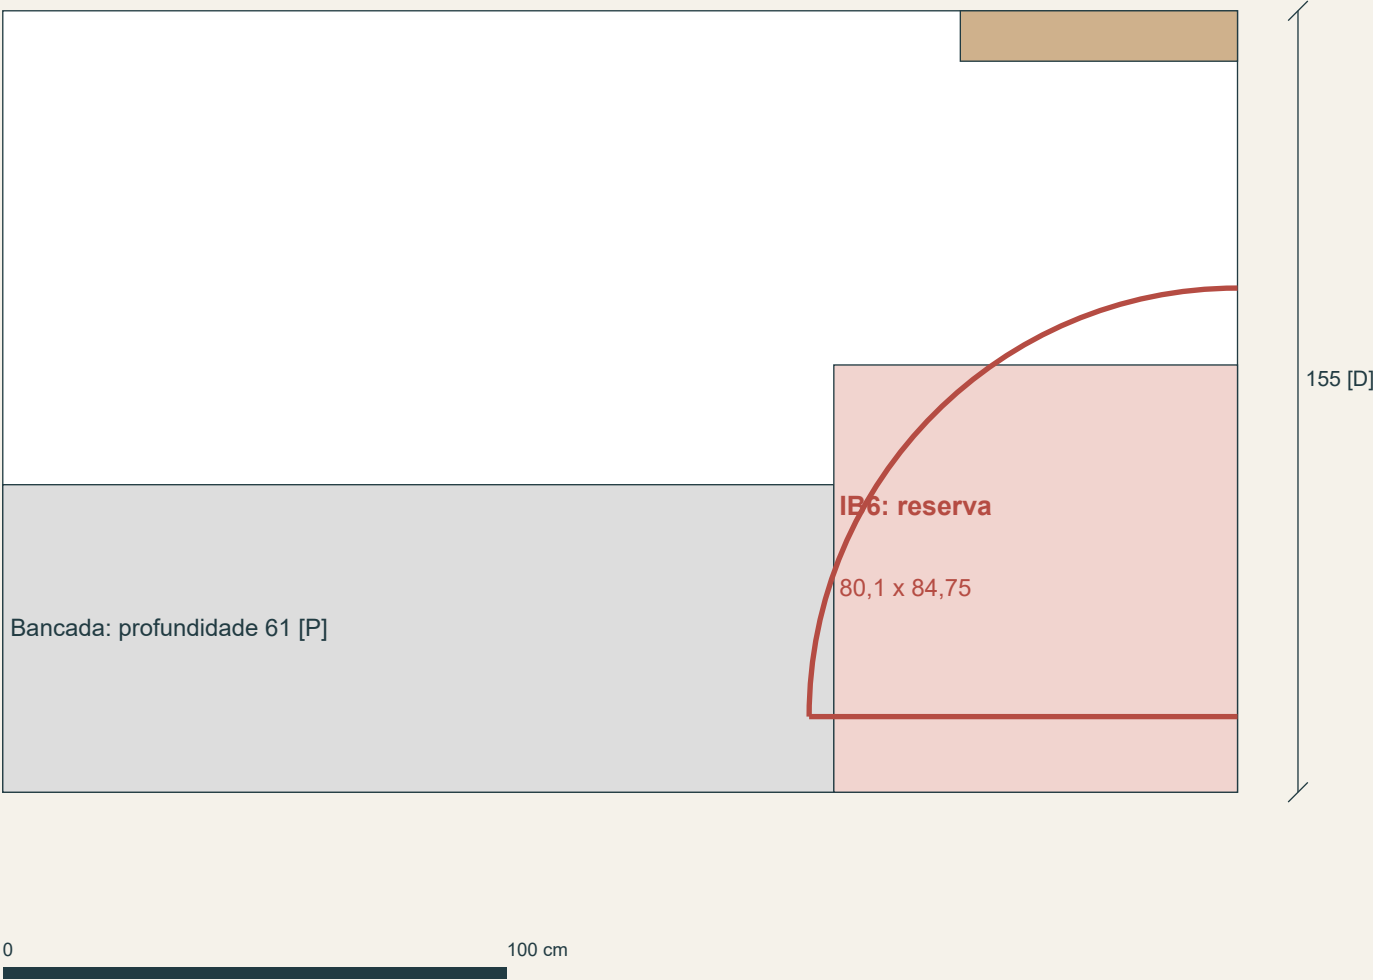

Porta aproximada: folha de 85 cm, com giro e dobradica lidos do desenho. Nao e vao util medido. O contorno oficial original deve prevalecer; o teste e de interferencia, nao projeto de alteracao da porta.

Interferencia material

No cenario extremo a direita, a reserva da geladeira ocupa x=164,9 a 245 e y=430,25 a 515. A folha aberta aproximada ocupa y=500, de x=160 a 245: cruza a reserva. Tambem resta pouca area para entrada com o equipamento fechado.

O que este estudo nao autoriza

Nao inverter porta, mudar gas, deslocar geladeira ou alterar sequencia de equipamentos sem compatibilizacao. Nao ha garantia de que manter o layout da imagem inicial resolva o conflito.

Proxima decisao tecnica

Resolver a faixa da entrada com o corpo real da IB6, suas folgas, abertura de portas e bancada. Depois recalcular o acesso inferior ao banco, a posicao do sofa e o lugar da chaise. As escolhas funcionais foram preservadas.

Outras pendencias reais


A terceira cadeira precisa de lugar cotidiano. Mesa/pedestal devem permitir tres cadeiras de um lado. A cama queen existente exige estudo proprio com dimensoes externas; nao foi substituida por uma cama menor. Nao foram definidos moveis do escritorio.

Conclusao

Prosseguir com 180 x 75 como hipotese principal do jantar. O encaixe e geometrico e condicionado; o layout completo ainda nao esta aprovado. Manter 92 cm como altura provisoria da pedra da cozinha, sem aplicar esse valor a mesa de jantar.


Cantos arredondados: raio proposto de 10 cm

Mesa 180 x 75 cm | Planta de verificacao em 1:10 no A3 a 100% | R10 e proposta, nao decisao fechada

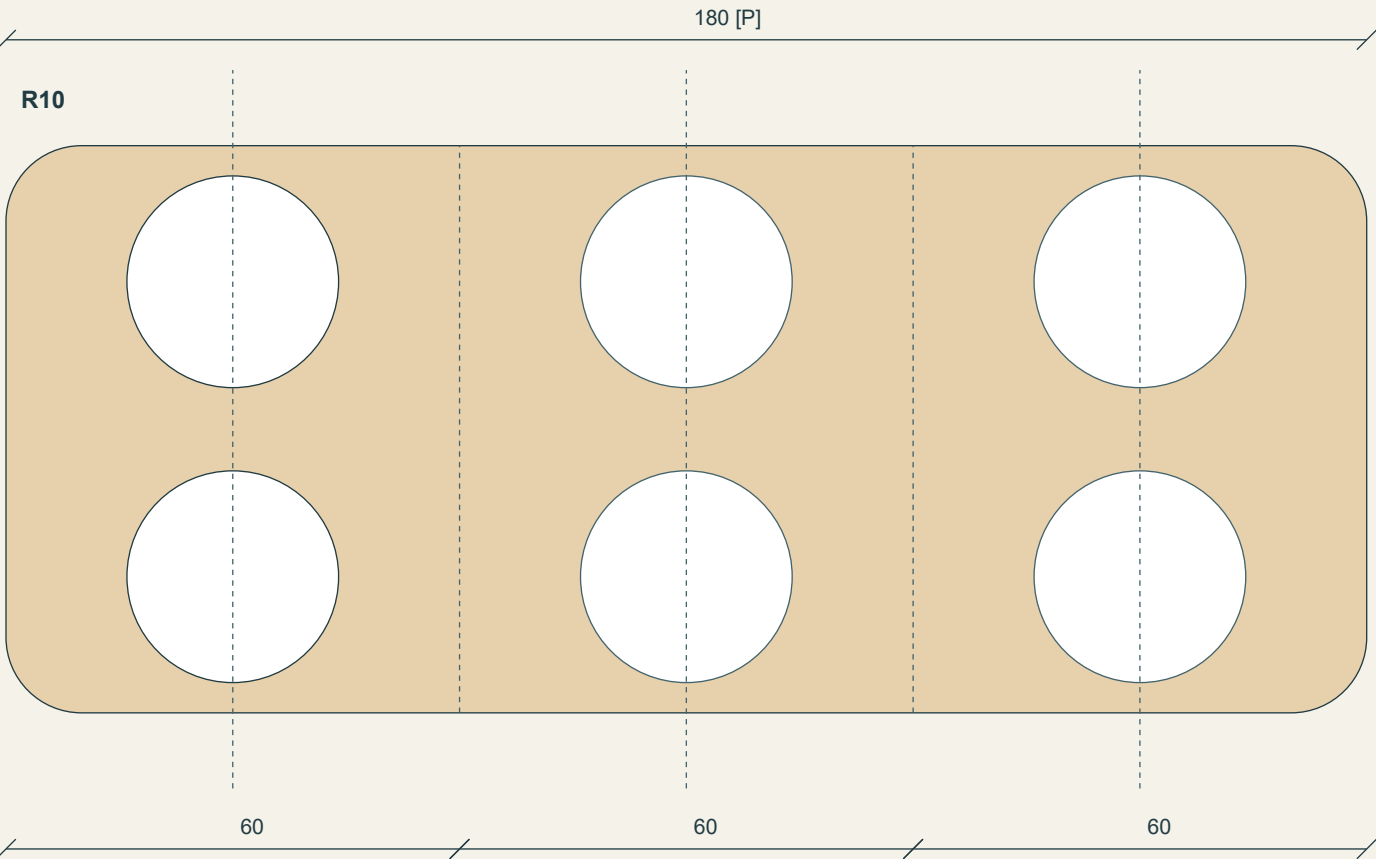

Seis pratos de 28 cm sao gabaritos de teste, nao inventario de Elias.

Centros a 30 / 90 / 150 cm; comidas servidas na bancada.

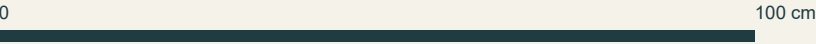

Area retirada e pequena; passagem principal permanece a mesma

Quatro cantos R10 retiram $(4 - \pi) \times 10^2 =$ aproximadamente 85,8 cm²: 0,64% de 13.500 cm² do tampo. Isso nao garante ergonomia, mas mostra que o efeito principal e retirar as pontas. A maior largura segue 75 cm e a faixa residual atras das cadeiras segue 65 cm no cenario anterior.

Raio, nao angulo de corte

O canto original vira um arco de 90 graus. O que determina quanto ele avanca no tampo e o raio: R10 cm = R100 mm. Um corte reto a 45 graus seria um chanfro, outra geometria.

O que permanece para sentar

Tres lugares continuam alinhados de cada lado. Ha 60 cm de passo entre centros. Com R10, a parte reta longa mede 160 cm e a curta 55 cm. Os lugares extremos ficam centrados fora das curvas; nao confundir 60 cm nominais com 60 cm de borda totalmente reta para cada pessoa.

Teste de superficie

Os seis circulos de 28 cm cabem no contorno proposto. Isso verifica apenas pratos. Cotovelos, copos, talheres, joelhos, pedestal e cadeiras precisam de ensaio; o desenho nao comprova conforto por duas horas.

Recomendacao

Comecar com R10 nos quatro cantos; R8 a R12 pode ser comparado no detalhamento. Evitar transformar automaticamente a mesa em oval completo: a curva ocuparia mais das extremidades. O raio final depende da amostra e da base escolhida.

IB6 confirmada novamente por Elias

Corpo: 60,1 cm de largura. Folgas laterais: 10 + 10 cm. Reserva corrigida: 80,1 cm, com paineis fora do vao. O erro anterior era de 1 cm. O desenho desta revisao foi corrigido; o conflito na entrada continua identificado. Teto informado de R\$ 3.600 mantido, sem compra ou preco garantido.