


Sofá-cama: a abertura é o limitante

Plantas 1:20 | Bancada lateral proposta, preservando janela e equipamentos sobre o tampo


A / cotidiano

295 cm

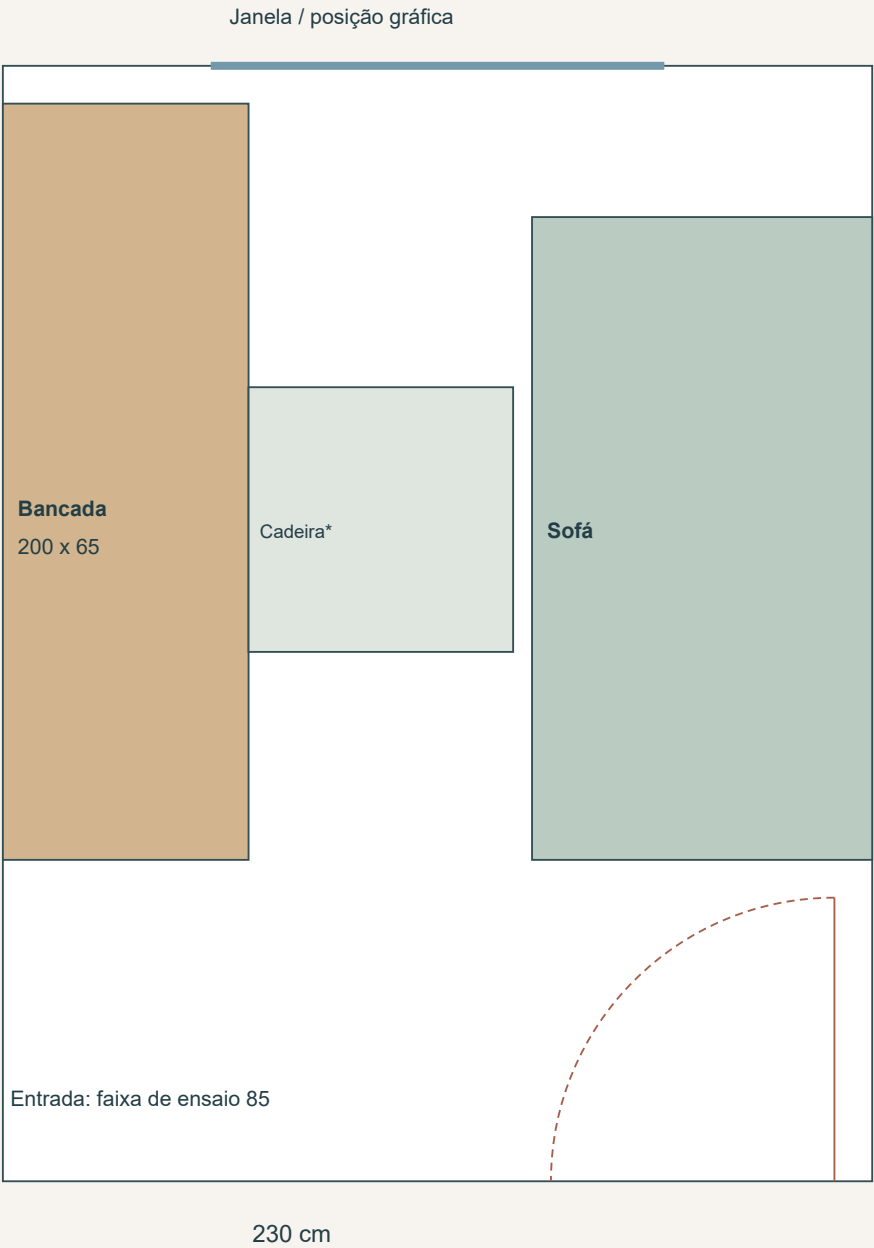

A / hóspedes

295 cm

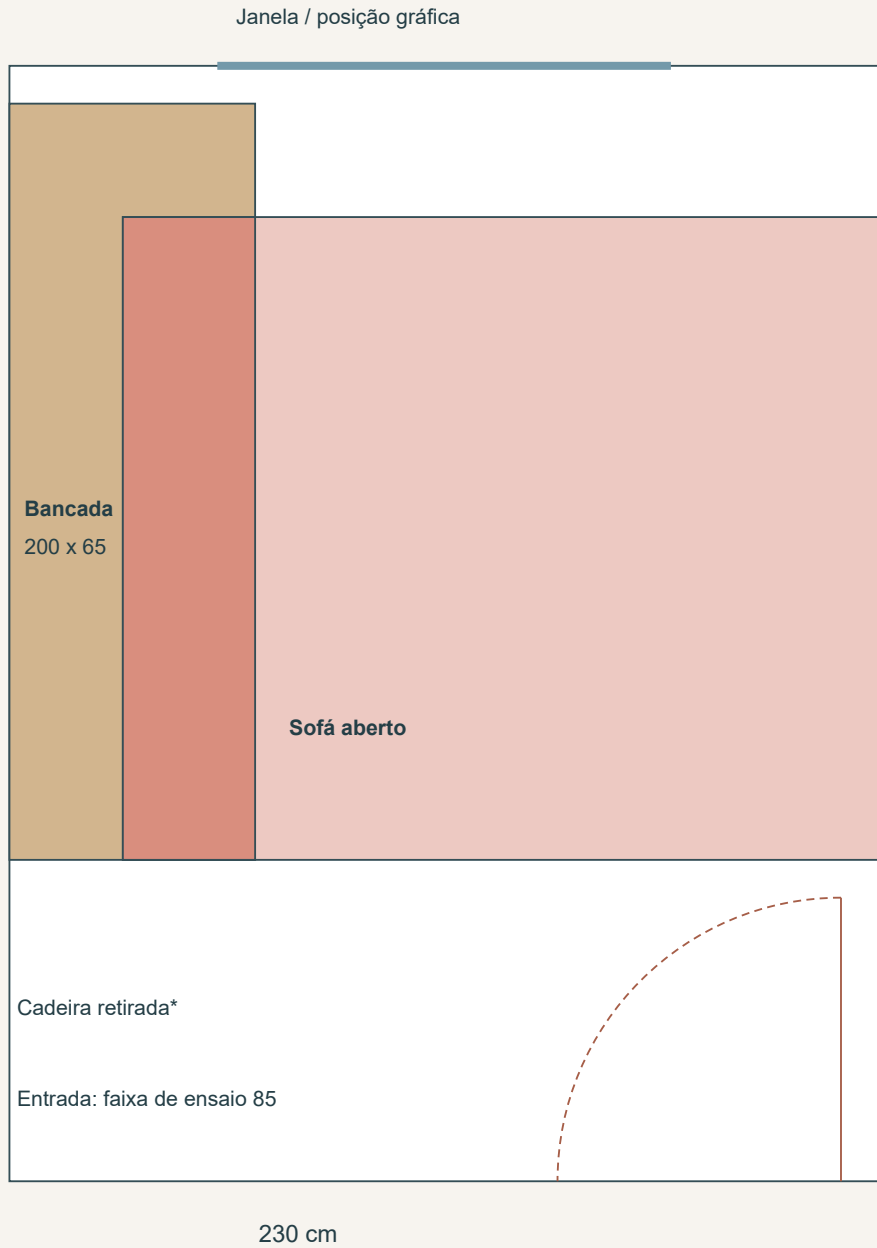

Envelopes testados
Bancada: 200 x 65.
Sofá fechado: 170 x 90.
Aberto: 170 ao longo da parede x 200 de projeção.

Resultado
Fechado, há 75 cm entre sofá e bancada. Aberto, o sofá cruza 35 cm do tampo. Este envelope não funciona.


Um sofá-cama diferente só entra nesta disposição se abrir até 155 cm de projeção, reservando 10 cm até a bancada. Isso é limite de busca, não prova de que exista modelo confortável para dois.

*Cadeira representada por envelope, não modelo. No modo hóspedes deverá ter local de guarda comprovado; não há destino de guarda aprovado. Porta: giro75 e posição aproximados da planta, não largura útil medida. Não alterar a porta para forçar cabimento.


Cama retrátil horizontal: melhor candidata para testar

Plantas 1:20 | Parede oposta à bancada; não exige retirar PC ou monitores neste envelope

B / trabalho
295 cm

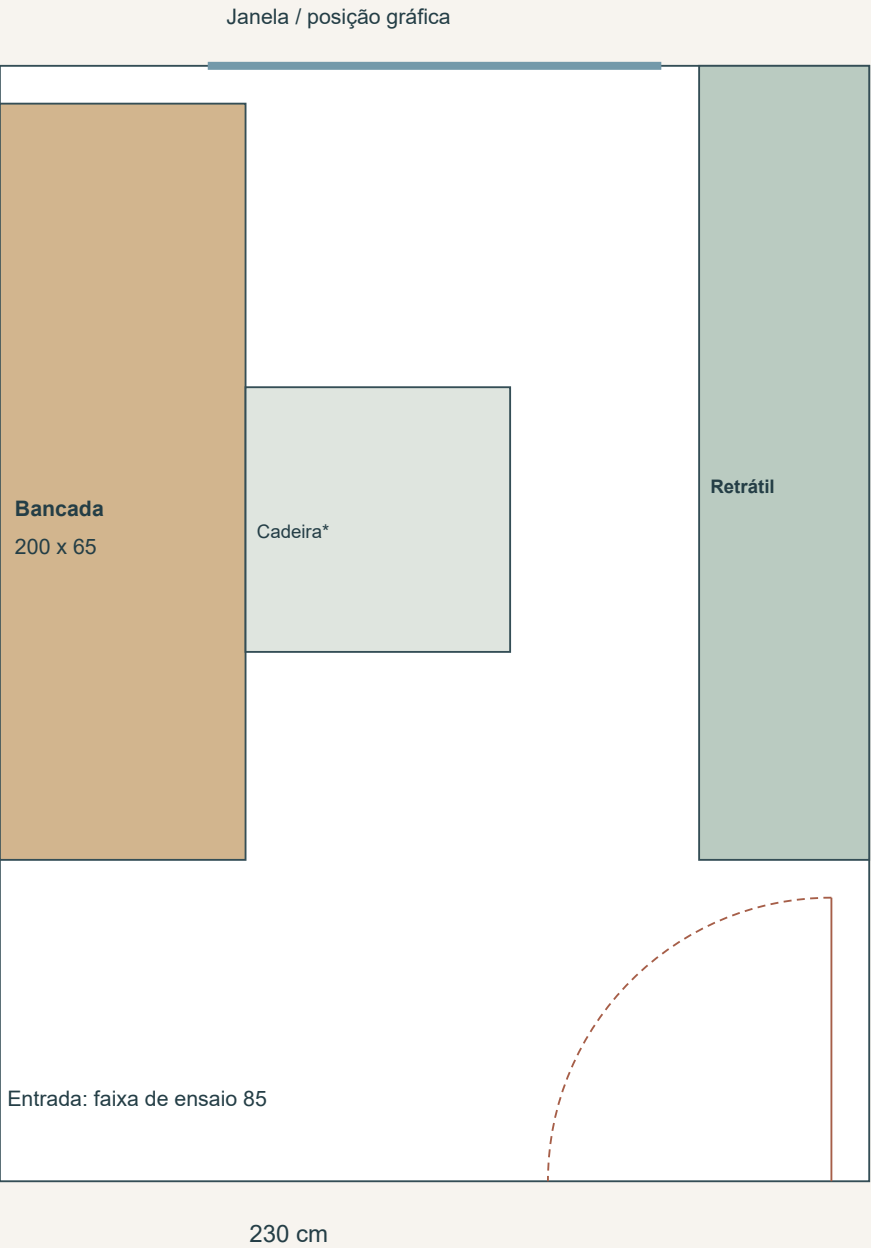

B / hóspedes
295 cm

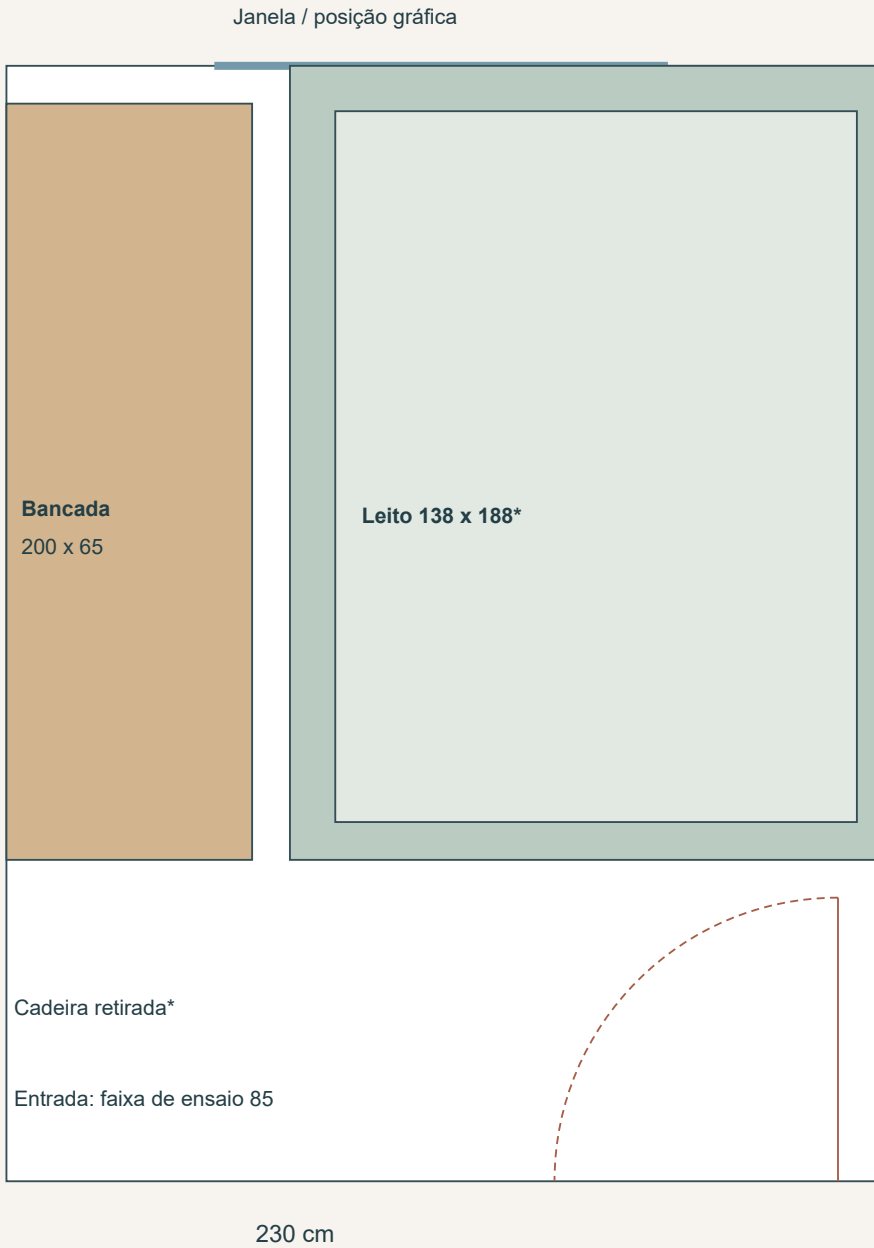

Módulo hipotético
210 cm ao longo da parede; 45 cm fechado; projeção total aberto até155 cm. Leito138 x188 apenas para testar dois lugares.


Trabalho
230 - 65 - 45 =120 cm entre bancada e móvel fechado. Cadeira de70 deixa50 cm atrás no envelope, não circulação certificada.

Hóspedes
230 - 65 - 155 =10 cm entre cama e bancada: não é corredor.
Entrada na cama pelos pés, pela faixa de85 cm. Estação sem uso.

Condição de compra: conferir dimensões externas, mecanismo em movimento, colchão e apoio com fabricante. P01 identifica alvenaria estrutural: não aprovar ancoragem sem validar parede e fixação. Cadeira deve sair da área da cama; destino ainda pendente, sem bloquear circulação externa.

Estação primeiro: o que a bancada precisa acomodar

Tampo em planta 1:10 | Dimensões de equipamentos abaixo são reservas de estudo, não inventário medido

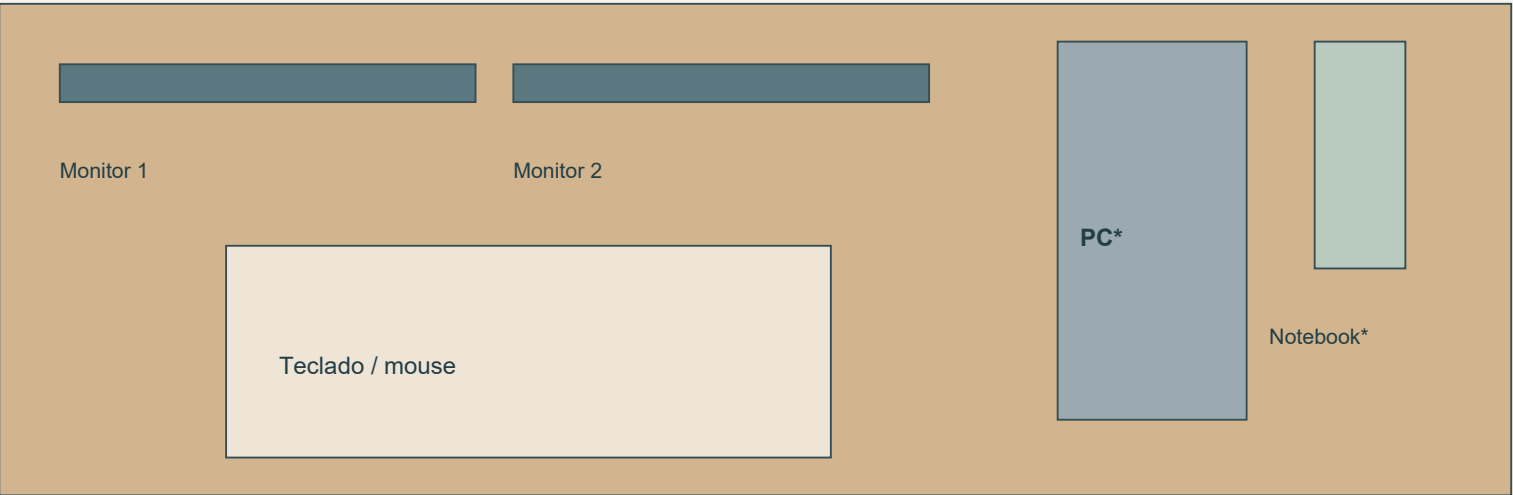

Volante removível
Montar na área central, deslocando teclado e mouse. Conferir fixação, espaço dos joelhos, pedais e estabilidade da cadeira. Prever guarda dedicada; volume não medido.

Janela e porta
Bancada lateral dá luz lateral às telas. Peitoril, abertura da janela, cortina, tomadas e pontos de rede ainda pendentes. Não usar a imagem de referência como levantamento.

200 x65 é a meta inicial
Duas telas com55 cm de largura cada, PC25 x50 e notebook fechado em suporte12 x30 foram simulados. Nenhuma dessas medidas substitui seu equipamento real.

Notebook fechado: só uma opção
Depende de conexão e regras do trabalho. Se precisar aberto como terceira tela, repetir o teste; não reduzir a área de teclado/mouse automaticamente.

Armazenamento
Priorizar módulos fechados acima da estação, após verificar altura de telas e cabeça. Evitar armário inferior que roube pernas. Não colocar nichos sobre o movimento da cama retrátil.

Conclusão
Retrátil horizontal é a direção preferida para pesquisar modelos. Sofá-cama segue alternativa se respeitar a projeção limite. TV permanece pendente; não reservar parede antes de resolver cama e estação.

Fonte: planta baixa oficial P01, Dormitório02 (2,30 x2,95); registro mestre ESC-001/002/003, F44 e F45. Área nominal6,785 m².