


O obstáculo anterior era a entrada mantida no lugar

Planta oficial ampliada | Marcas sobre a geometria original; sem escala de execução

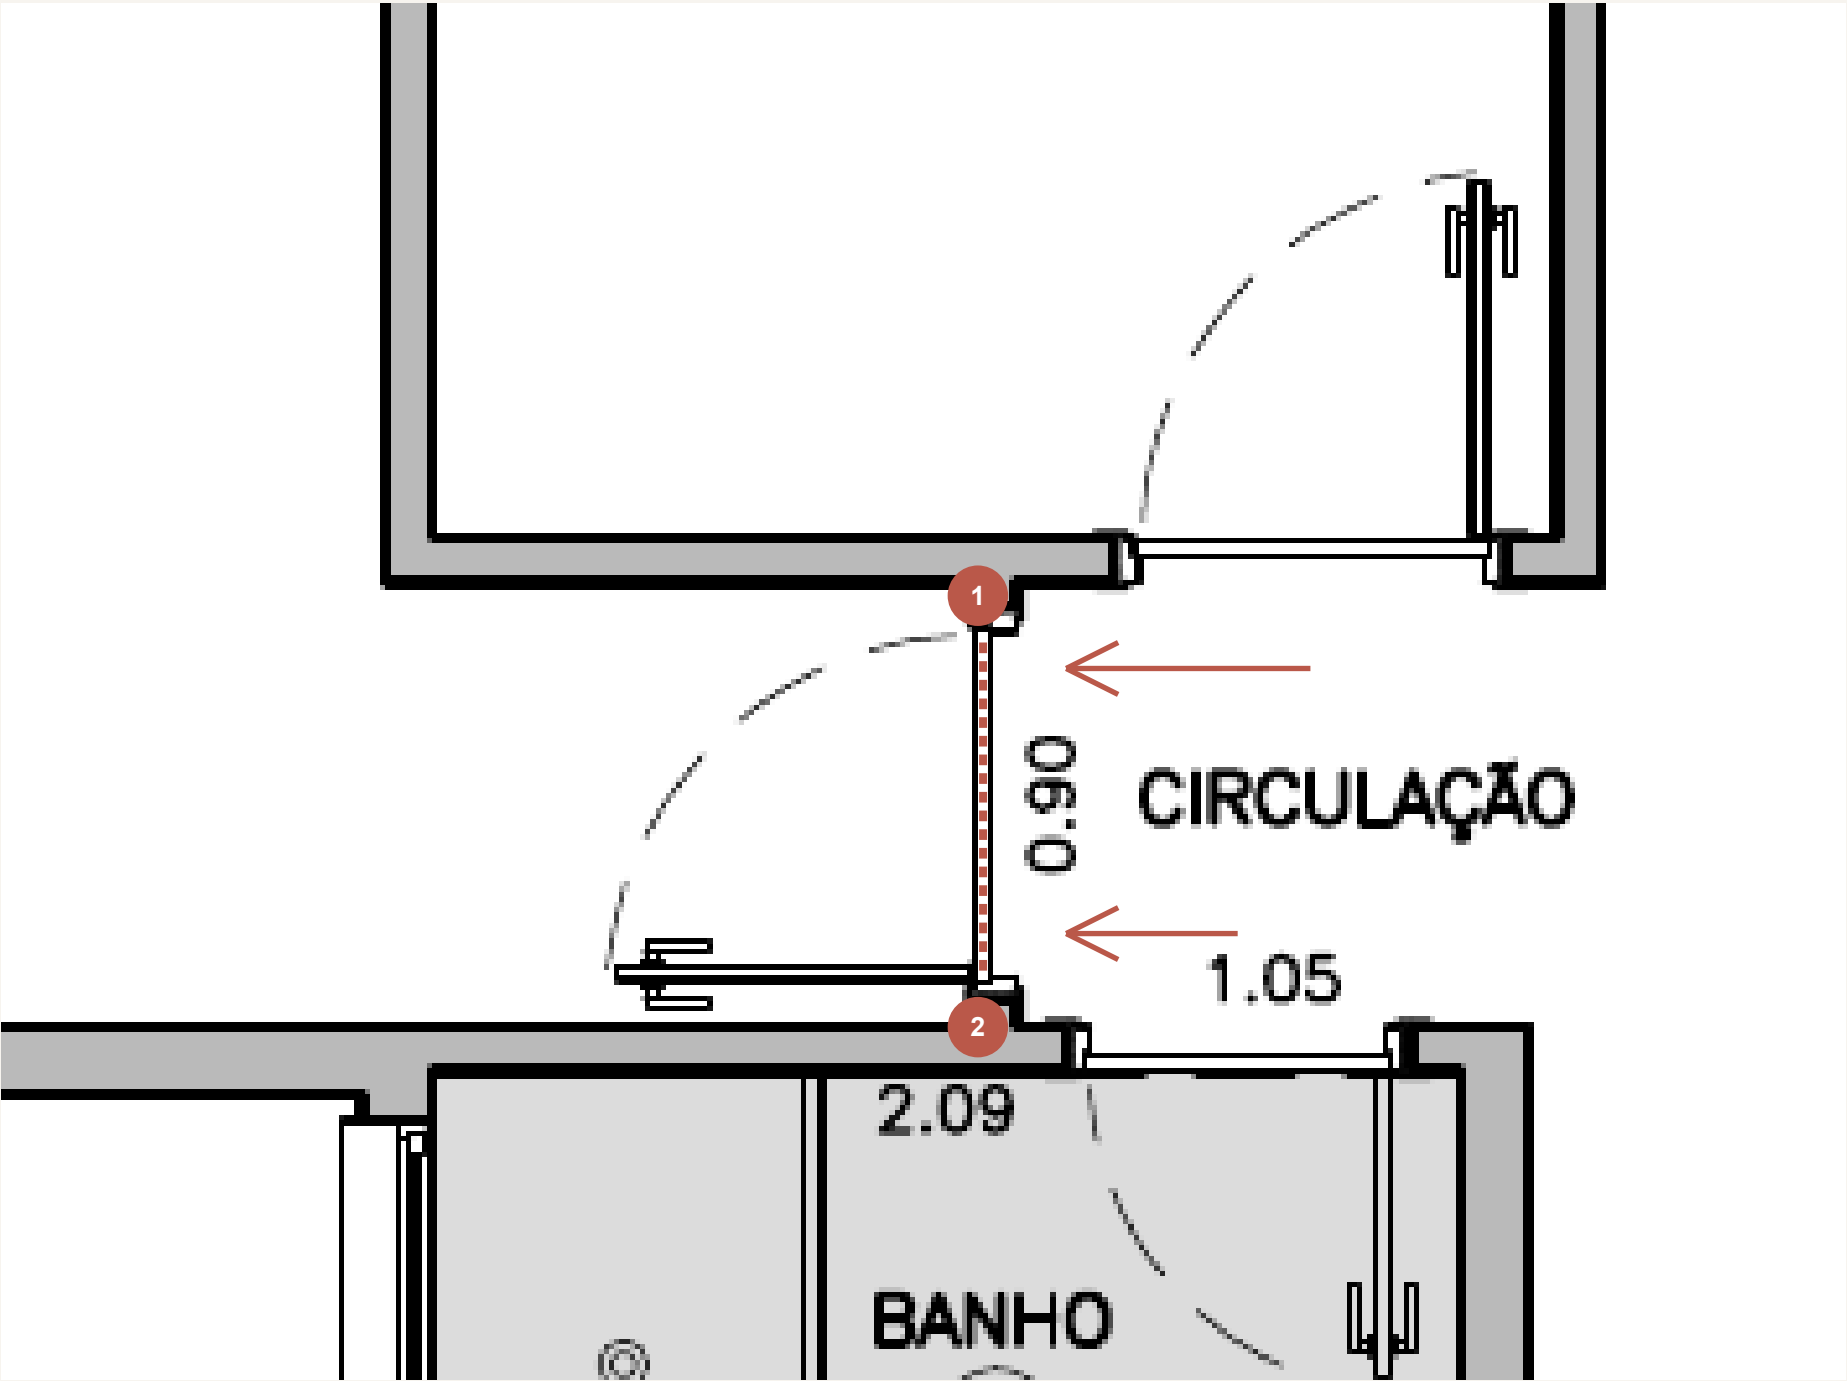

1 e 2 / extremidades do vão antigo
São os encontros que precisam ser conferidos para a folha passar rumo ao dormitório. A planta não permite separar com segurança batente removível, acabamento e eventual ressalto de alvenaria.


O que o R00 considerava
A entrada do quarto permanecia nesta posição. O percurso das portas externas terminava nesse encontro. A conclusão não contemplava recuar a entrada como Elias agora propôs.

Correção de interpretação
Não tratar toda essa região como parede estrutural a demolir. Pode haver batente removível, mas isso exige conferência. A legenda da planta identifica alvenaria estrutural; remover batente não autoriza cortar os encontros de parede.

Vermelho: passagem antiga e encontros a verificar. Setas: direção desejada para recolher as portas externas. A proposta de recuo é apresentada na página 2.

Sua proposta de recuo merece avançar no estudo

Hipótese: novo fechamento perto do guarda-roupa, mantendo o corredor prolongado até ele

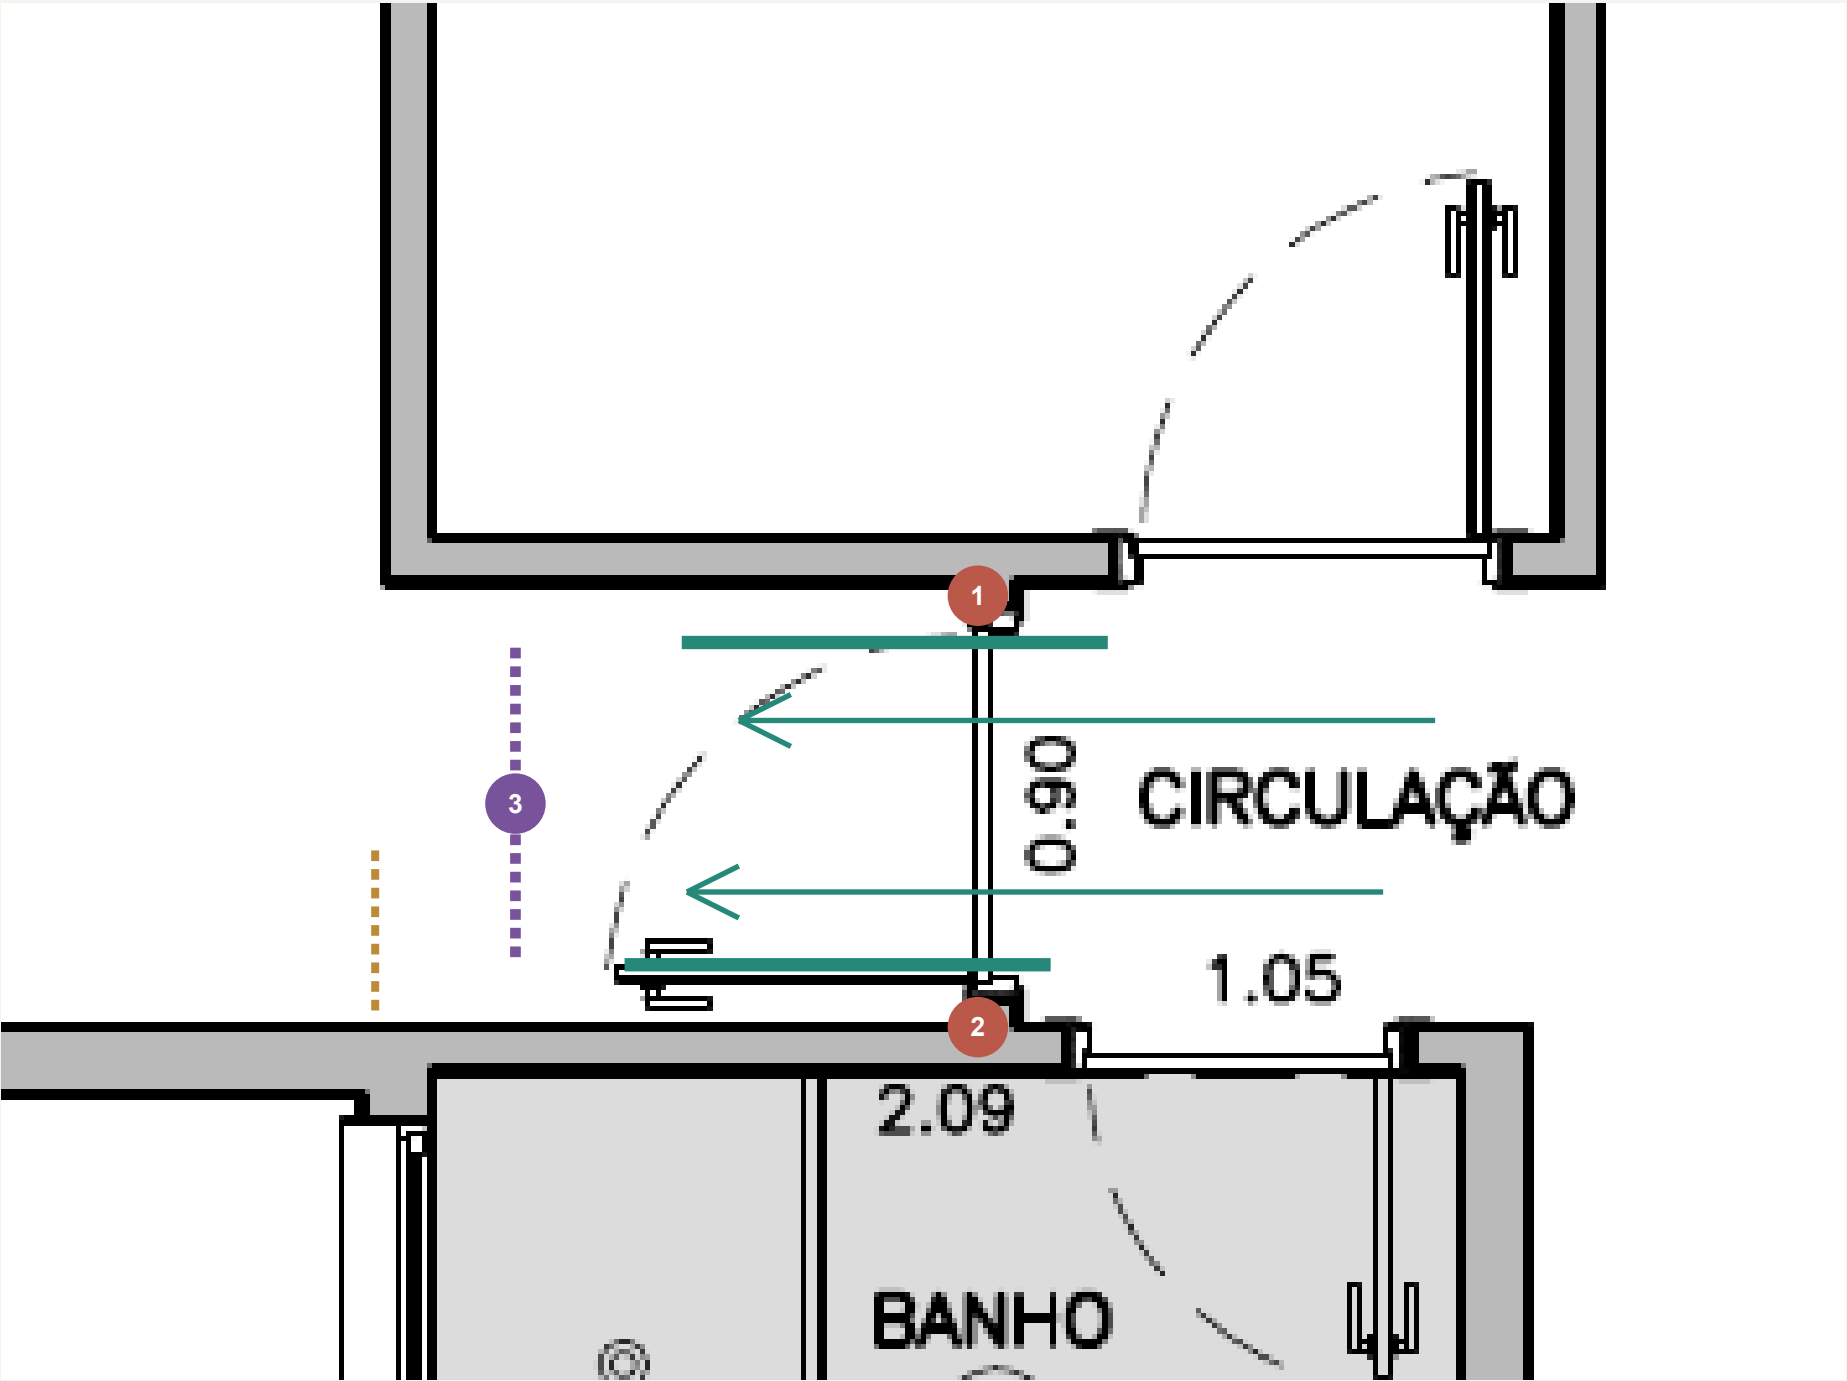

Verde / folhas abertas rumo ao quarto
Ao recuar o fechamento, existe comprimento gráfico para estudar as duas folhas recolhidas nas faces opostas do corredor prolongado. Elas não precisam ocupar o mesmo plano.

3 / nova entrada do dormitório
Linha roxa: posição apenas indicativa, a ajustar ao guarda-roupa e à passagem. Marca o fechamento, não uma porta de correr já resolvida. Tipo e movimento da nova porta ainda precisam ser testados.

O que pode impedir o encaixe
Ressaltos 1/2, distância da folha à parede, puxadores, guias e novo batente. O limite do guarda-roupa (traço ocre) vem da referência visual, não de marcenaria medida.

Corredor
Exemplo: 90 cm documentais menos 6 cm de cada sistema = 78 cm entre folhas. Os 6 cm são hipótese, não produto escolhido nem largura aprovada.

Os giros originais permanecem visíveis apenas como base histórica. Nenhuma parede foi apagada. Verde e roxo representam estudo, não obra aprovada. O recuo transfere parte da entrada privativa do quarto para a circulação.

Porta articulada: onde existe ganho de uso

Alternativa com duas folhas dobráveis | Esquema matemático, não produto ou ferragem escolhidos



Giro: projeção até 75 cm*

Articulada: até 37,5 cm*

*Exemplo ideal de 75 cm dividido em duas folhas iguais. Mecanismo real, espessura e puxadores alteram o resultado. A pilha dobrada ocupa parte do vão: verificar a passagem útil do conjunto.

Recomendação

Não descartar as duas portas externas antes de verificar a proposta de recuo. Se ela exigir intervenção estrutural ou estreitar demais a circulação, estudar articulada primeiro no banheiro. No escritório, decidir pelo conflito real com o móvel de hóspedes; no quarto, evitar a troca sem benefício demonstrado.

Fontes: planta oficial P01; referência visual quarto1.png (mobiliário não medido); registro F49. Princípio da porta dobrável: Pormade, artigo de 07/02/2024. Pesquisa em 11/09/2026.

Fonte técnica: blog.pormade.com.br/2024/02/07/porta-camarao/

1 / Banheiro: maior ganho cotidiano provável
Reduz a invasão do giro na aproximação da pia e na entrada. Testar primeiro dobrando para dentro, sem avançar no corredor. Conferir pia, fecho de privacidade, umidade e passagem útil.

2 / Escritório: ganho condicional
Facilita a manobra perto da porta. No R01, a reserva de cama de 140 x 210 já não cruzava o giro hipotético. A articulada não libera, por si, uma cama maior nem resolve a guarda da cadeira.

3 / Quarto: menor ganho comprovado
No vão atual, o giro ocupa principalmente o recuo de entrada. Só compensa se atrapalhar a passagem ou o guarda-roupa. Na nova entrada recuada, testar novamente com o armário real.