


Seis lugares: encaixe possivel, ainda condicionado

Base oficial + hipoteses explicitas | Escopo: jantar, interface com sala, cozinha e entrada

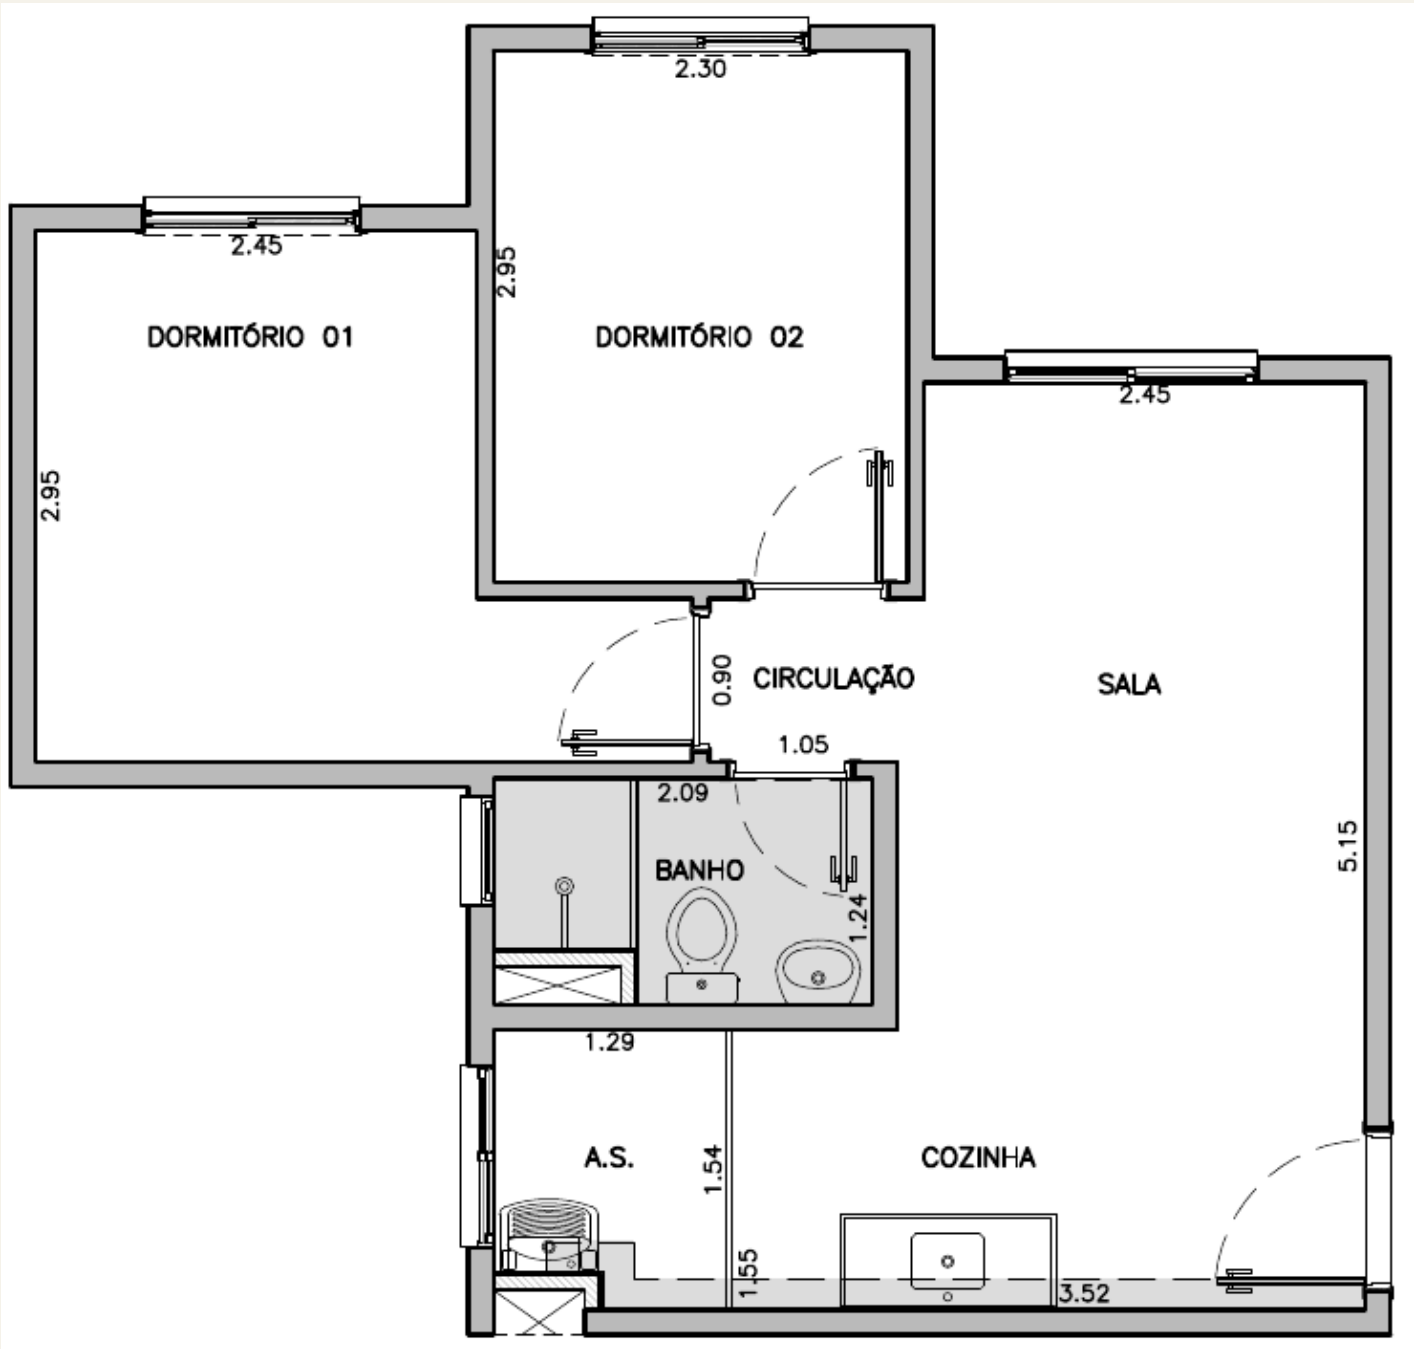

Recorte da planta oficial, apenas para leitura: sem escala de impressao nesta pagina.

O que foi conferido

A cota 245 corresponde a largura superior da sala. A cota 515 vai da parede da janela ate a parede da cozinha: nao e comprimento exclusivo de sala e jantar. A propria planta admite variacoes pelos acabamentos.

Resultado principal

Mesa fixa proposta de 180 x 75, banco reto de 180 x 55 e tres cadeiras sem bracos. O conjunto cabe geometricamente na faixa conservadora de 245, mas deixa apenas 65 atras das cadeiras no cenario sentado adotado. Nao equivale a conforto validado para duas horas.

Restricao encontrada



A reserva da geladeira no extremo junto a entrada se sobrepoe ao giro grafico da porta neste teste. A interface cozinha/entrada precisa ser resolvida antes de aprovar o layout completo. Nenhum equipamento ou ponto foi alterado.

Como ler as medidas

[D] cota documental. [P] proposta de movel ou envelope de uso. [G] estimativa grafica. [C] calculo condicionado as hipoteses. Somente as pranchas 2 e 4 possuem escalas fisicas declaradas; imprimir A3 a 100%, sem ajustar.

Uso diario e seis pessoas sentadas

Plantas esquematicas em escala 1:25 no A3 a 100% | Todas as dimensoes de moveis sao propostas

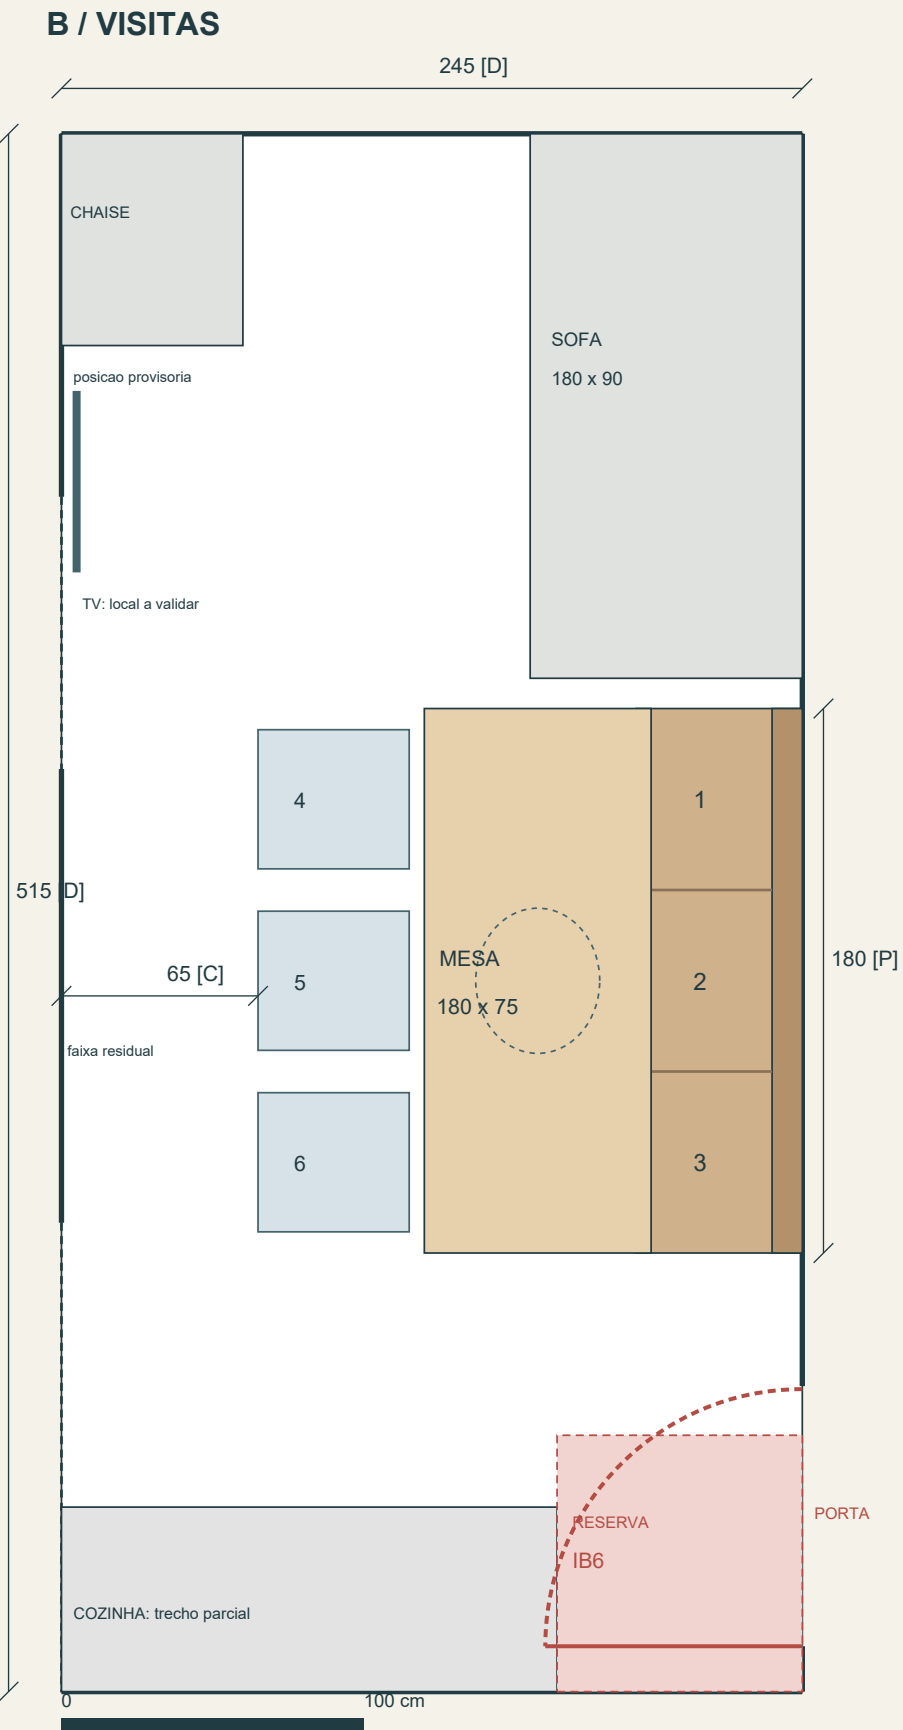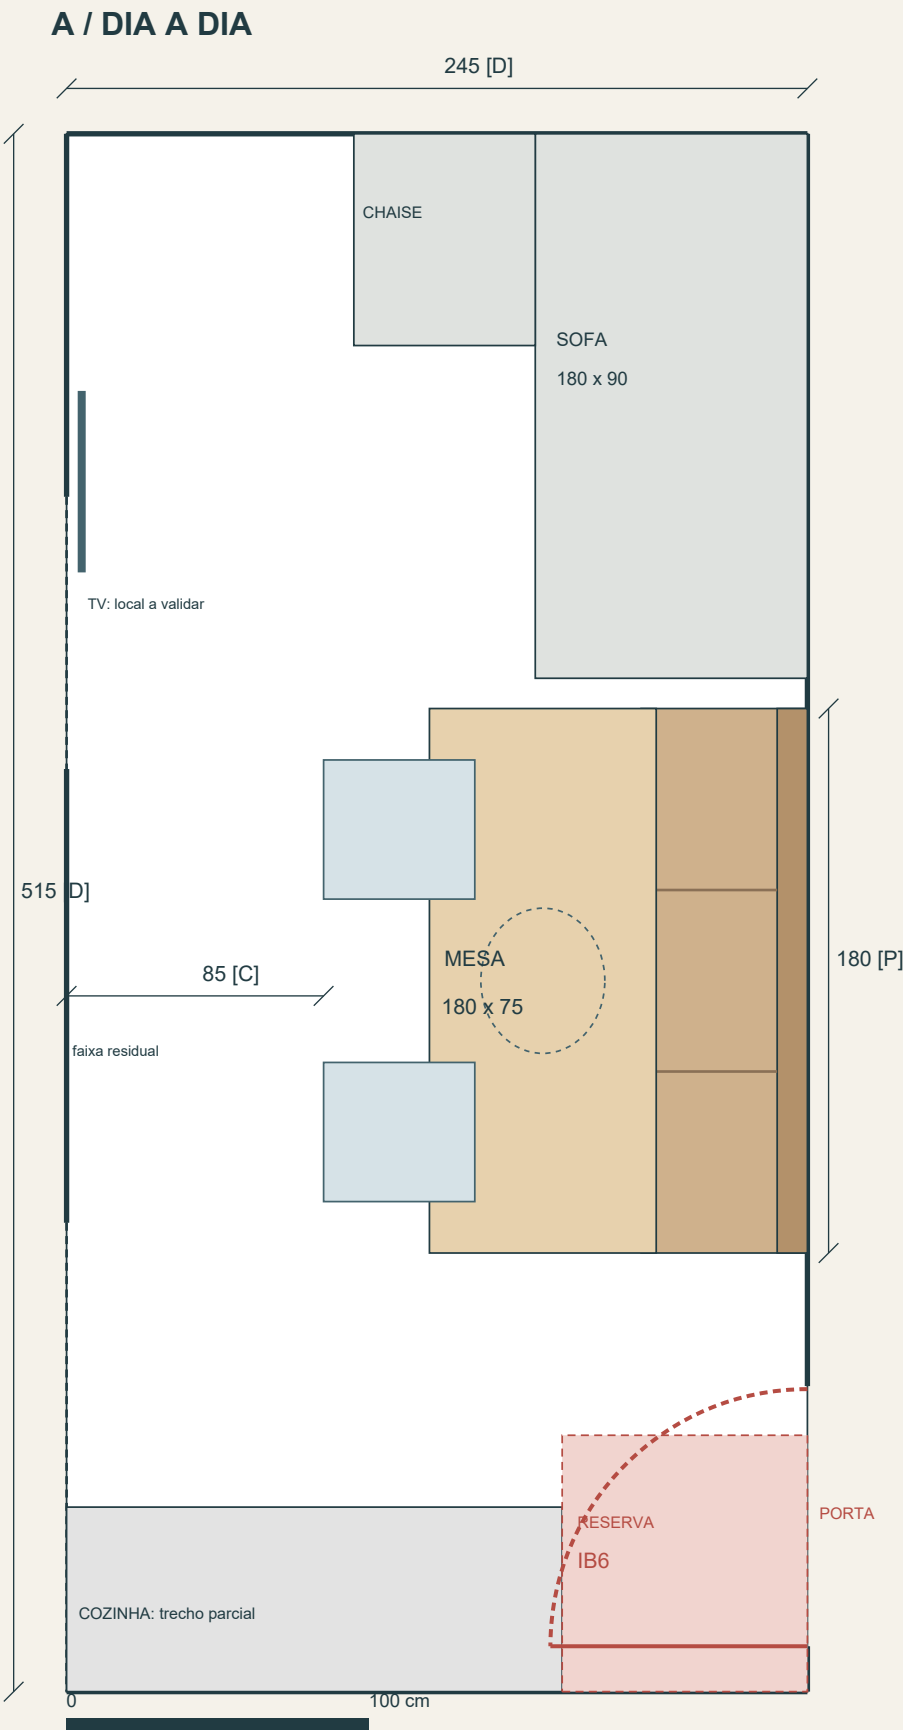

85 cm no modo recolhido

245 - 50 (parede a borda) - 75 (tampo) - 35 (cadeira recolhida) = 85. Nao representa duas pessoas sentadas. Ao usar uma cadeira, aplicar o envelope ocupado.

65 cm no modo ocupado

Com 55 da borda da mesa ate as costas da pessoa/cadeira: 245 - 50 - 75 - 55 = 65. Passagem apertada; nao e rota acessivel nem aprovacao normativa.

Tres pessoas no banco

180 / 3 = 60 de frente nominal por pessoa. Banco com 55 totais, sendo 10 reservados ao encosto e 45 ao assento. Estofamento, altura e cantos podem reduzir o uso real.

Acesso pelo lado da cozinha

Banco vai de y=190 a y=370. Reserva IB6 inicia em y=430,25: intervalo de 60,25. Essa aproximacao depende da posicao final da geladeira; o conflito na entrada impede valida-la.

Sala e terceira cadeira

Sofa 180 x 90 e chaise 60 x 70 sao envelopes de teste. A chaise deslocada fica provisoriamente junto a janela. Terceira cadeira fora deste recorte no cotidiano: ambiente ainda nao definido. TV nao tem destino aprovado.

Medidas propostas e limites de conforto

Comparacao numerica | Mesma parede a borda de 50 cm e envelope ocupado de 55 cm

Comparacao das mesas fixas

Tampo [P]	Frente/pessoa [C]	Faixa residual [C]	Leitura
160 x 75	53,3 cm	65 cm	Mais curta; pior para 3 alinhados.
180 x 70	60 cm	70 cm	Ganha 5 cm; tampo mais estreito.
180 x 75	60 cm	65 cm	Melhor equilibrio inicial; condicionado.
180 x 80	60 cm	60 cm	Mais apoio, pior passagem.
190 x 75	63,3 cm	65 cm	Consome mais 10 cm longitudinais.

Sensibilidade: o corpo e a cadeira mudam o resultado

Com tampo de 75, um envelope ocupado de 50 / 55 / 60 cm deixa respectivamente 70 / 65 / 60 cm. Se a largura real for 240, com envelope de 55, a faixa cai para 60 cm. Se banco e borda precisarem avançar mais 5 cm, perde-se mais 5 cm. Nao contar o recuo grafico do banheiro como folga garantida.

Movimentar a mesa tem um custo

Afastar a mesa 15 cm da parede para facilitar entrada no banco reduz a faixa ocupada de 65 para 50 cm. Com uma cadeira recuada mais 25 cm para levantar, sobram 40 cm no mesmo alinhamento. Portanto, entrada/saida e passagem nao podem ser consideradas simultaneamente confortaveis. Reposicionar com lugares desocupados e recolher depois.


Critérios usados, sem transformar recomendacao em norma

Adotados 60 cm de frente por pessoa e envelopes de cadeiras explicitamente propostos. A referencia comercial Room & Board recomenda 18-24 polegadas por lugar (aprox. 46-61 cm) e 36 polegadas de folga ao redor da mesa (aprox. 91 cm); sao orientacoes de mobiliario, nao normas brasileiras. Neste arranjo, mesa ate limite oposto = 120 cm; descontar pessoa/cadeira e indispensavel para avaliar passagem real.

Fonte: roomandboard.com/design/inspiration/dining-kitchen/how-to-design-a-dining-room | consulta 10/09/2026

Entrada: interferencia que impede fechar o conjunto

Detalhe em escala 1:15 no A3 a 100% | Porta por leitura grafica; reserva IB6 transcrita do quadro A04.4

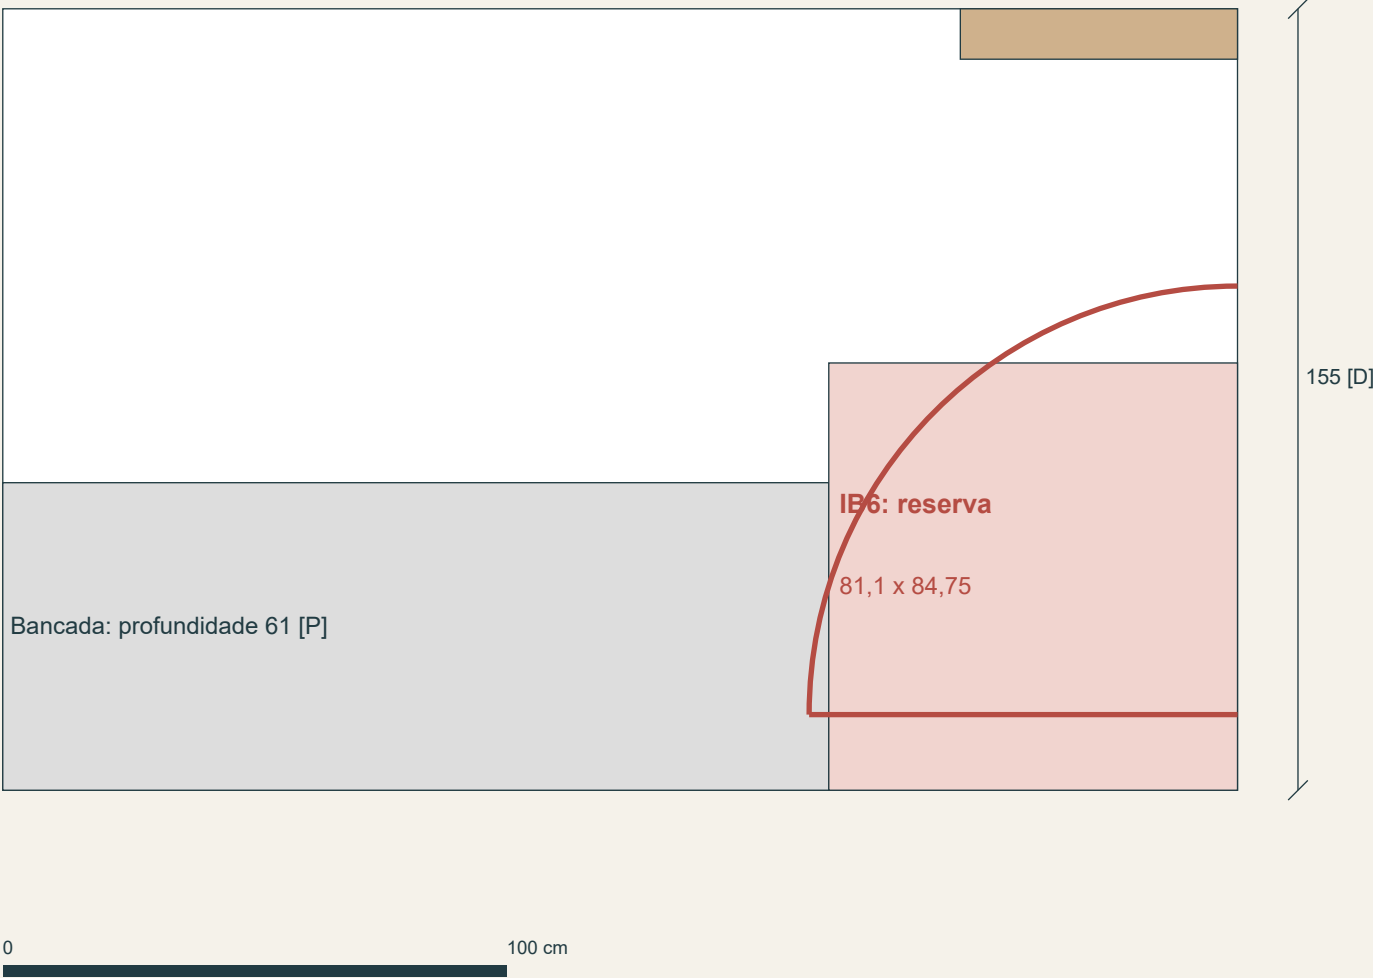

Porta aproximada: folha de 85 cm, com giro e dobradica lidos do desenho. Nao e vao util medido. O contorno oficial original deve prevalecer; o teste e de interferencia, nao projeto de alteracao da porta.

Interferencia material

No cenario extremo a direita, a reserva da geladeira ocupa x=163,9 a 245 e y=430,25 a 515. A folha aberta aproximada ocupa y=500, de x=160 a 245: cruza a reserva. Tambem resta pouca area para entrada com o equipamento fechado.

O que este estudo nao autoriza

Nao inverter porta, mudar gas, deslocar geladeira ou alterar sequencia de equipamentos sem compatibilizacao. Nao ha garantia de que manter o layout da imagem inicial resolva o conflito.

Proxima decisao tecnica

Resolver a faixa da entrada com o corpo real da IB6, suas folgas, abertura de portas e bancada. Depois recalculer o acesso inferior ao banco, a posicao do sofa e o lugar da chaise. As escolhas funcionais foram preservadas.

Outras pendencias reais

A terceira cadeira precisa de lugar cotidiano. Mesa/pedestal devem permitir tres cadeiras de um lado. A cama queen existente exige estudo proprio com dimensoes externas; nao foi substituida por uma cama menor. Nao foram definidos moveis do escritorio.

Conclusao

Prosseguir com 180 x 75 como hipotese principal do jantar. O encaixe e geometrico e condicionado; o layout completo ainda nao esta aprovado. Manter 92 cm como altura provisoria da pedra da cozinha, sem aplicar esse valor a mesa de jantar.